



KONCEPCE KRAJINY Semněvic

/ ATELIER SALZMANN-BEČVÁŘOVÁ-POZDECH /
/ ZS 2023 / FA ČVUT /
autorky : GRUNTOVÁ; JÍROVCOVÁ; KVAPILOVÁ;
KOUPALOVÁ; MORAVCOVÁ; PURMOVÁ; KUNCÍŘOVÁ

závěry analýz území

problémy

- technicky upravené toky (narovnané, zahloubené, zpevněné)
 - lokální problémová místa
 - 1 čerpa sklidka odpadů
 - 2 neuspokojivé rozhraní sídla a krajiny
 - 3 území pro novou výstavbu bez potřebných regulativ na charakter
 - 4 jerní bliskové povodně
 - odvzdušňovací meliorace ve vztahových oblastech vodních toků
 - největší zemědělská lesy
- PROBLÉMY BEZ ÚZEMNÍHO PRŮMĚTU**
nevýhledová kanalizace → znečišťování vody / negativní zásahy do vodního režimu (neodolnost povrchu vrtů) / neekologičnost dlouhodobého plánování / nedostatečná bezmotorová dostupnost území

hodnoty a potenciály

- trasy historických cest
 - přírodní a kulturní hodnoty**
 - 5 pozůstatky hradeb po dvou rybářských
 - 6 bývalý lom a ohradním obvodem
 - 7 pomník padlým v 1. a 2. světové válce
 - 8 socha sv. Jana Nepomuckého
 - 9 "Společná zpráva"
 - kostel sv. Jiří
 - kaple
 - křížky volně stojící
 - výhledové náhledové plochy
 - centrální výhledy
- HODNOTY A POTENCIÁLY BEZ ÚZEMNÍHO PRŮMĚTU**
malost krajiny a příjemný krajní ráz / romantická krajinná struktura / odlišná krajina vyznívá v místy zastavěném území / území bez velkých změn od 19. st. /



SHRNUTÍ PROBLÉMU
Jako nejdůležitější význam problémy spojené s vodním režimem. Roztřísnění znečištění → této oblasti území ohrožena ziská krajina budoucnost stabilnější.

obora Čertůvka

KONCEPCE

Jelím cílem bylo krajinu uchopit komplexně, jako jeden celek, a stanovit principy a způsoby racionálního a udržitelného využití a zásahů, tak aby prosperovala a dobře se v ní lidé žilo.

cestní síť

Stávající cestní síť není chudá, ale často špatně napojená, vedoucí od nikud nikam. Obyvatelé chodí svou trasou a zbytek je jim cizí, chtějí do krajiny, ale nemají jak. Cílem proto bylo nejen dostat lidi do krajiny, ale hlavně navštívit krajinu lidem.

Nás návrh spočívá v těchto bodech:

- propojení vesnic
- zastávky bodů zájmu (Křížky, kapličky, výhledy, vodní plochy, pramenitě, lom)
- vhodné vedení cest (vodní toky, hranice polí, obnova zaniklých cest)
- vložení cestní zeleně (biodiverzita, zadání vody, větrology, estetika)
- zpřístupnění okolí obce (Sedmihoří, turistika, cyklo, okolí vesnic)
- zpřístupnění lesů a obor

sídla

- chytřejší koncepce odpadních vod
- nalézt udržitelné a souběžné ekologické řešení
- hospodárení se sražkovou vodou v obcích
- stanovení rozvojových ploch
- vymezení ploch a charakteru veřejných prostranství
- společenský život v obcích

kulturní a historické hodnoty

zemědělství

- menší zemědělské plochy
- větší propojenost zelení
- udržitelné hospodárení
- udržování půdy
- respekt k vodě v krajině

přírodní pokryv



vodní režim

Kvůli nevhodným zásahům v minulosti je vodní režim v území poškozený a postupně se stává nefunkčním. V této vrstvě jsme se snažili co nejvíce navrhnout vhodný způsob.

Jak snížit negativní dopady odvodňovacích opatření a postupnými citlivými zásahy vodu do krajiny vrátit.

- podpora a ochrana vztahových oblastí vodního toku
- zadržování vody v krajině
- obnova vodních toků

morfologie terénu

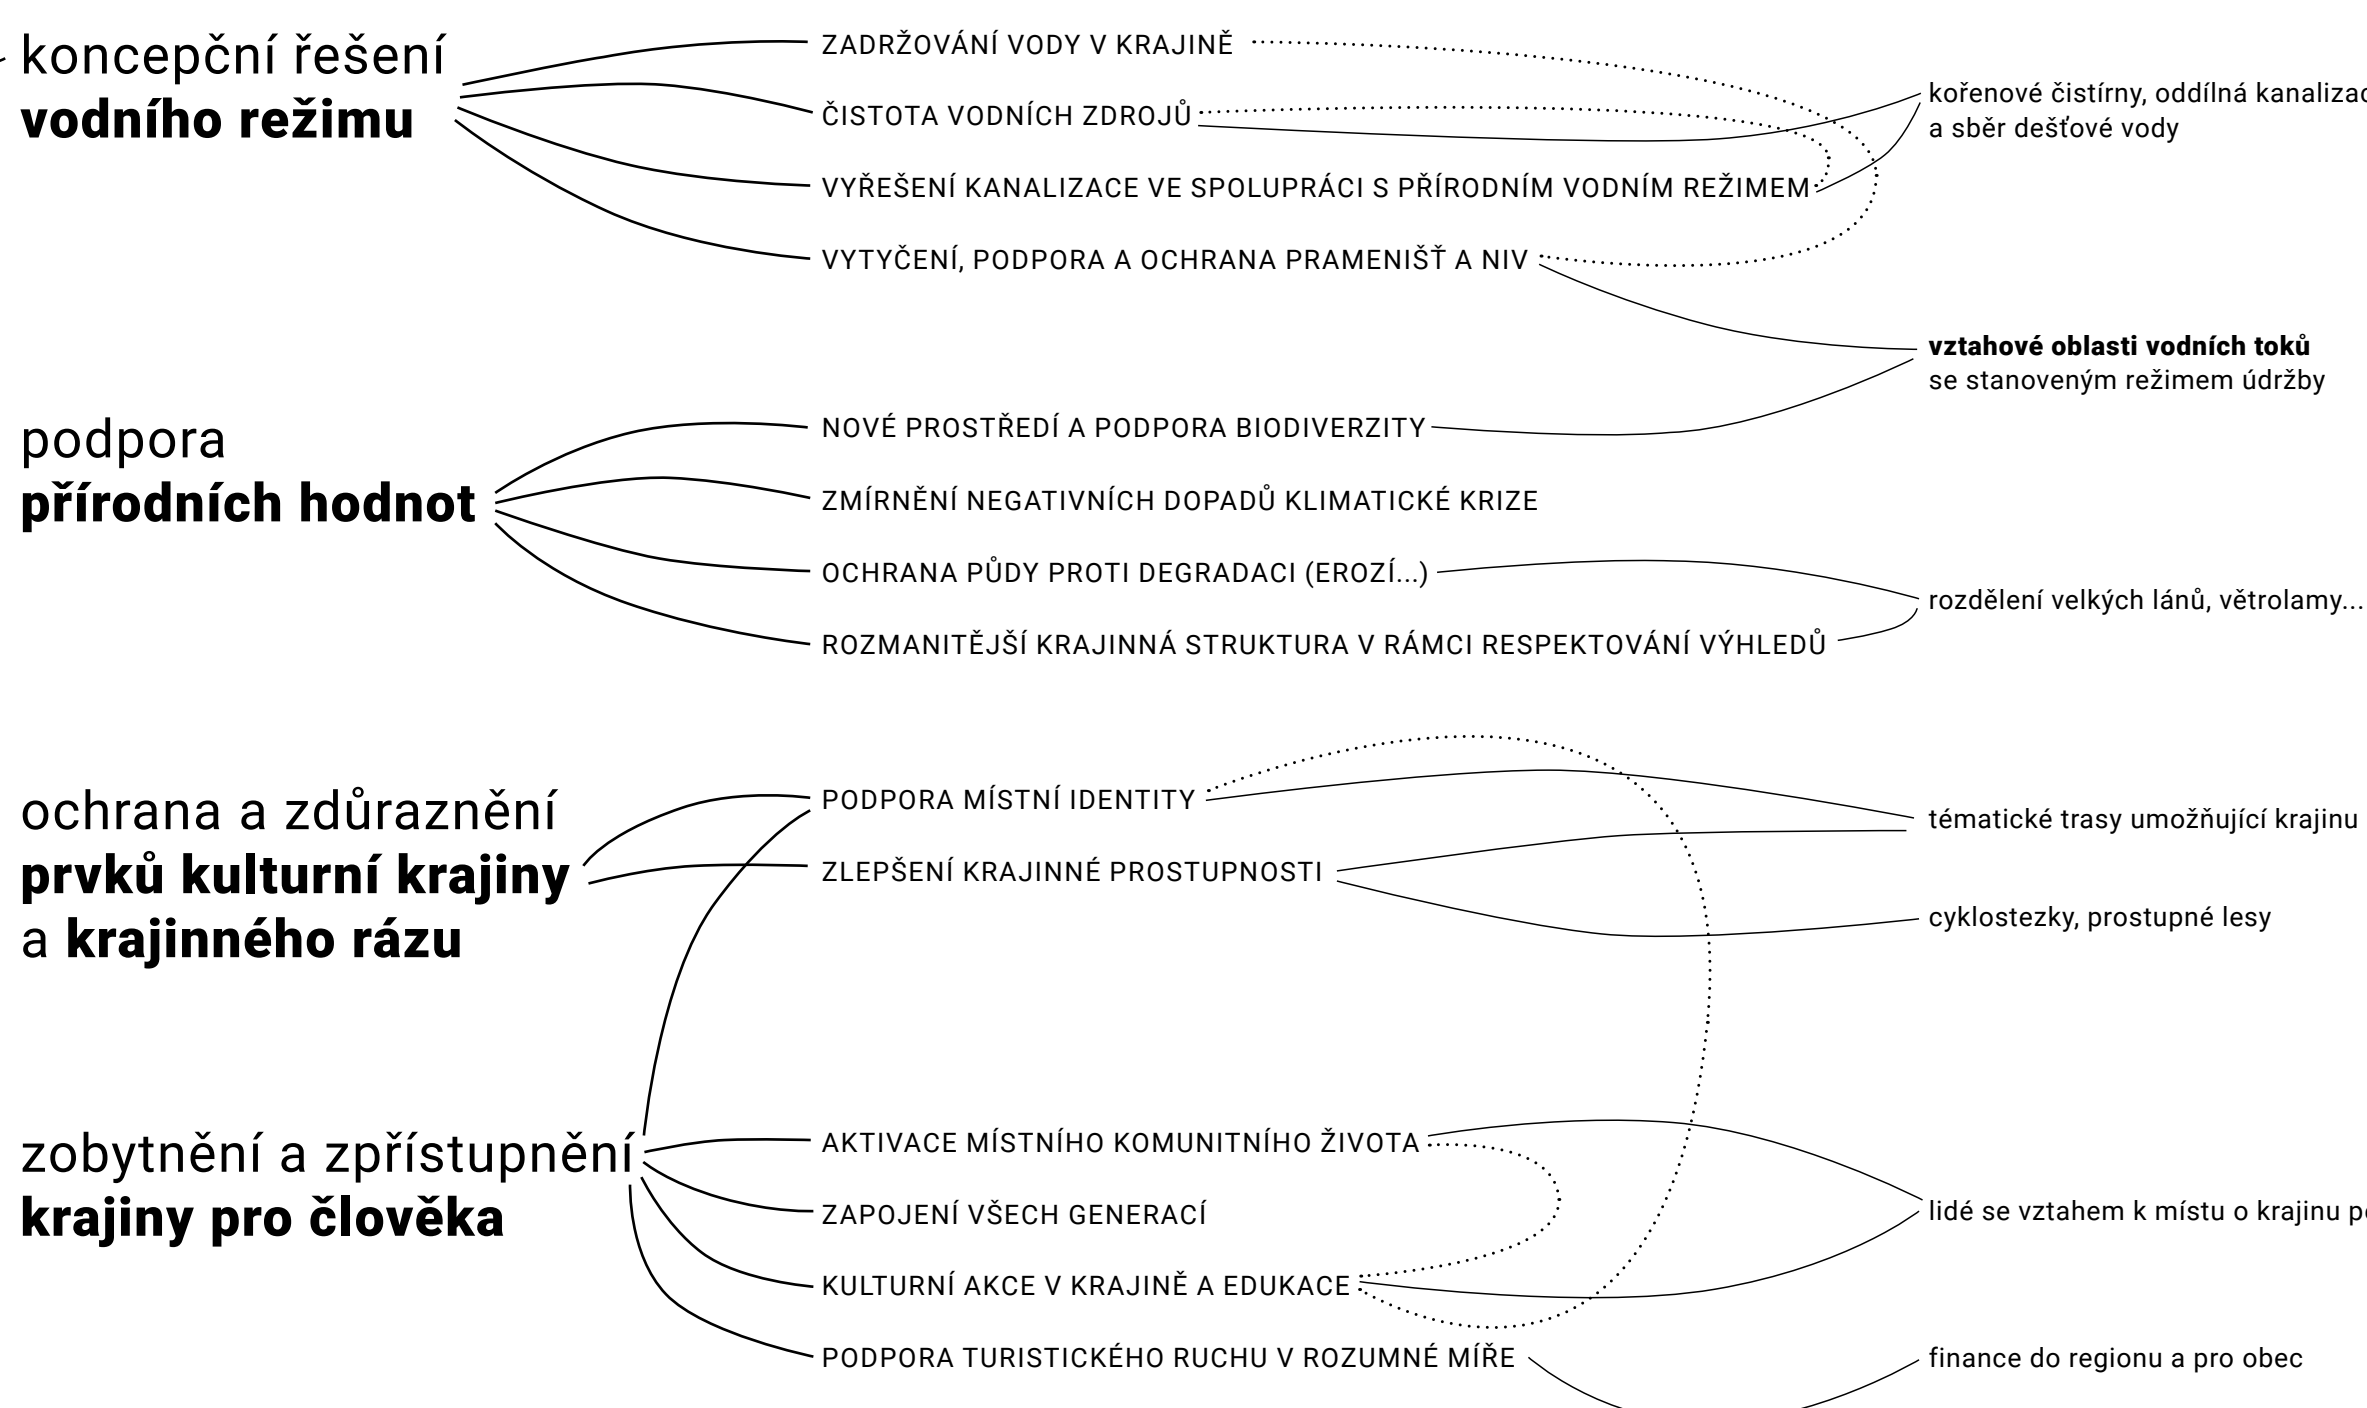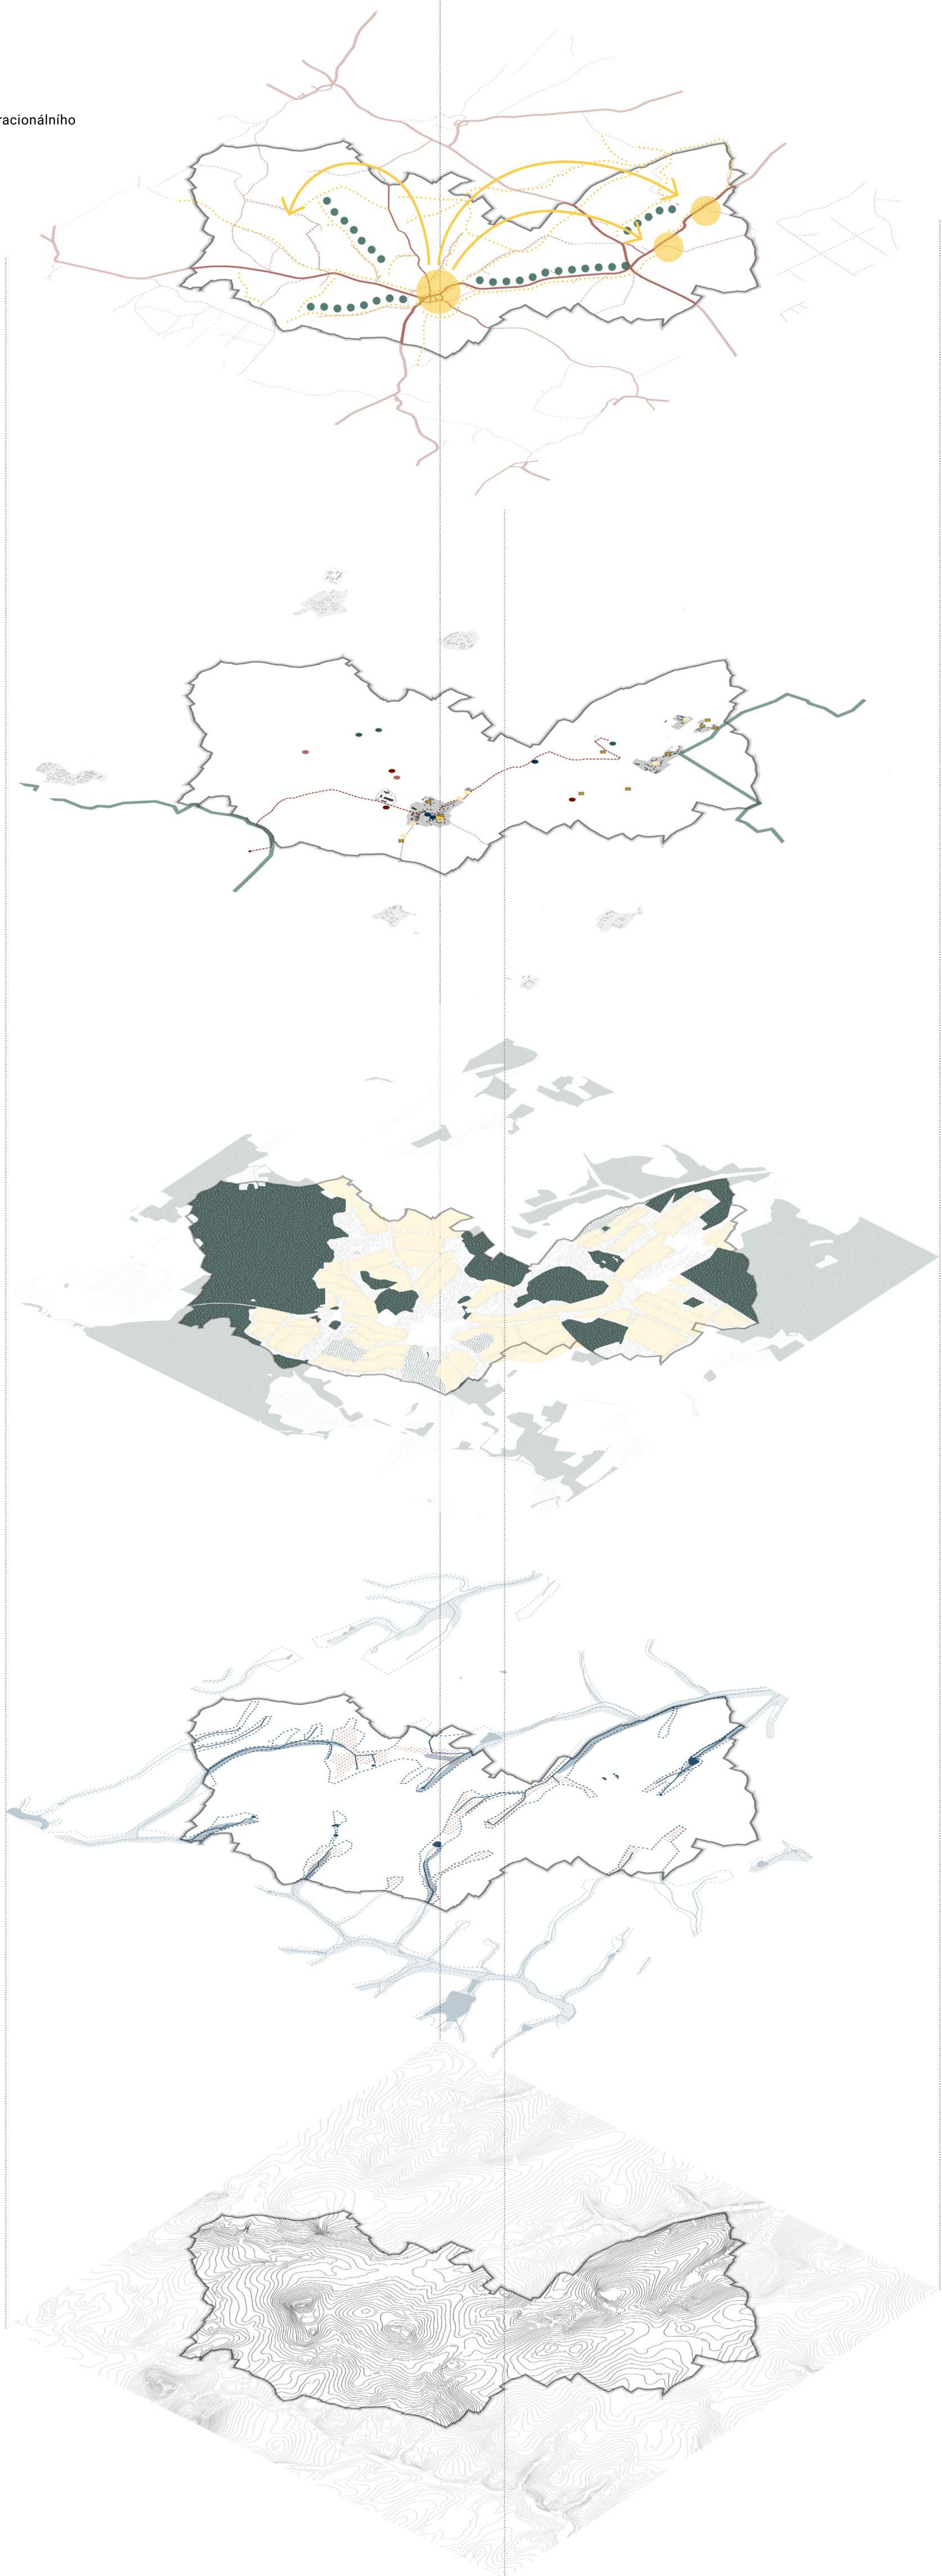

LEGENDA :

- KONVENČNÍ ZEMĚDĚLSTVÍ
- OKOLOGICKÉ ZEMĚDĚLSTVÍ
- AGROLESNICKÝ SYSTÉM
- ZEMĚDĚLSKÉ PLOCHY
- SAD S LOUKOU
- ZELĚN
- SILNICE
- NAVŘZENÁ CESTA
- STÁVAJÍCÍ CESTA
- NAVŘZENÁ CYKLO
- STÁVAJÍCÍ CYKLO
- TRAVNÍ PÁS
- NAVŘZENÉ STROMODŘADÍ
- OBNOVA SILNIČNÍ ALEJE
- NAVŘZENÝ VOLNÝ POROST
- KŘÍŽEK
- KAPLIČKA
- AUTOBUSOVÁ ZASTÁVKA
- VÝSLAČ
- VROCHOL
- ZASTAVĚNÉ ÚZEMÍ
- VEŘEJNÉ PROSTORY
- LOUKA
- LES
- VZTAHOVÁ OBLAST V.T.
- ÚPRAVA V.T.
- BUFFER ZONE
- PROSTOR VODY MINIMÁLNÍHO ZÁSAHU
- PROSTOR VODY VĚTŠÍHO ZÁSAHU