

ZUZANA PURMOVÁ
portfolio

CURRICULUM VITAE

PERSONAL INFO

zuzana.purmova@gmail.com
+420 721 152 711



date of birth 16.7. 2001

education 09/2016 - 06/2020 Akademické gymnázium Štěpánská [gymnasium]
(Štěpánská 614, 110 00, Praha)

09/2020 **Czech technical university in Prague, Faculty of Architecture**
(Thákurova 9, 160 00, Praha)
study programme: **Landscape Architecture**

06/2023 the bachelor’s degree successfully ended

09/2023 starting the master’s studies

01/2025 - 06/2025 **Erasmus stay at Lund University**

06/2026 expected completion of the master’s degree

languages **English - level C1** (the FCE certification)
French - level B1

skills **software** (AutoCAD; Rhino; QGIS; Adobe Photoshop, Illustrator and InDesign)
various handwork and art techniques



A SKETCH FROM JESENÍKY MOUNTAINS

December 2025

INTRODUCTION

The aim of this portfolio is to show various types of scales and topics that I have worked with, and to describe the process of my practice through selected designs.

The presentation starts with the scale of landscape planning, and with each project, we zoom in to the most detailed one.

Enjoy!

ALL OF MY PROJECT WITH COMPLETED MATERIALS IN HIGH RESOLUTION :
<https://www.fa.cvut.cz/en/gallery/portfolio/18416-zuzana-purmova/atelierove-prace>



A SKETCH FROM VYSOČINA REGION



A SKETCH FROM TRIP TO SLOVENIA

REWATERIZATION

The task arises from the demand of the Semněvice municipality, which covers approximately 12 km² in the southwest of the Czech Republic. Their aim was to start developing the area conceptually, so the municipality needed to obtain some strategies concerning the landscape and natural environment in general.



That is why we proposed a vision and a landscape concept based on an analysis of the territory. Its aim was to grasp the landscape as a whole and to establish principles and methods for rational and sustainable use, so that it could thrive and people could live well in it.

The REWATERIZATION project is the final part, done individually by me. For the detailed demonstration of the principles set in the landscape concept, I chose a specific location where a technical water reservoir is planned. The design there offers a more suitable alternative that will improve the local environment more comprehensively.


The first part of the project was done in a group, where we, after understanding the territory through a complex analysis, proposed a vision to establish the main directions and intentions.

Then we projected these general ideas onto the area, creating the landscape concept plan. Proposing specific interventions, it contained suggestions for changes in land-use, new connections, etc.

The final part was the individual work, where we selected a smaller area and showed how the design works in detail.

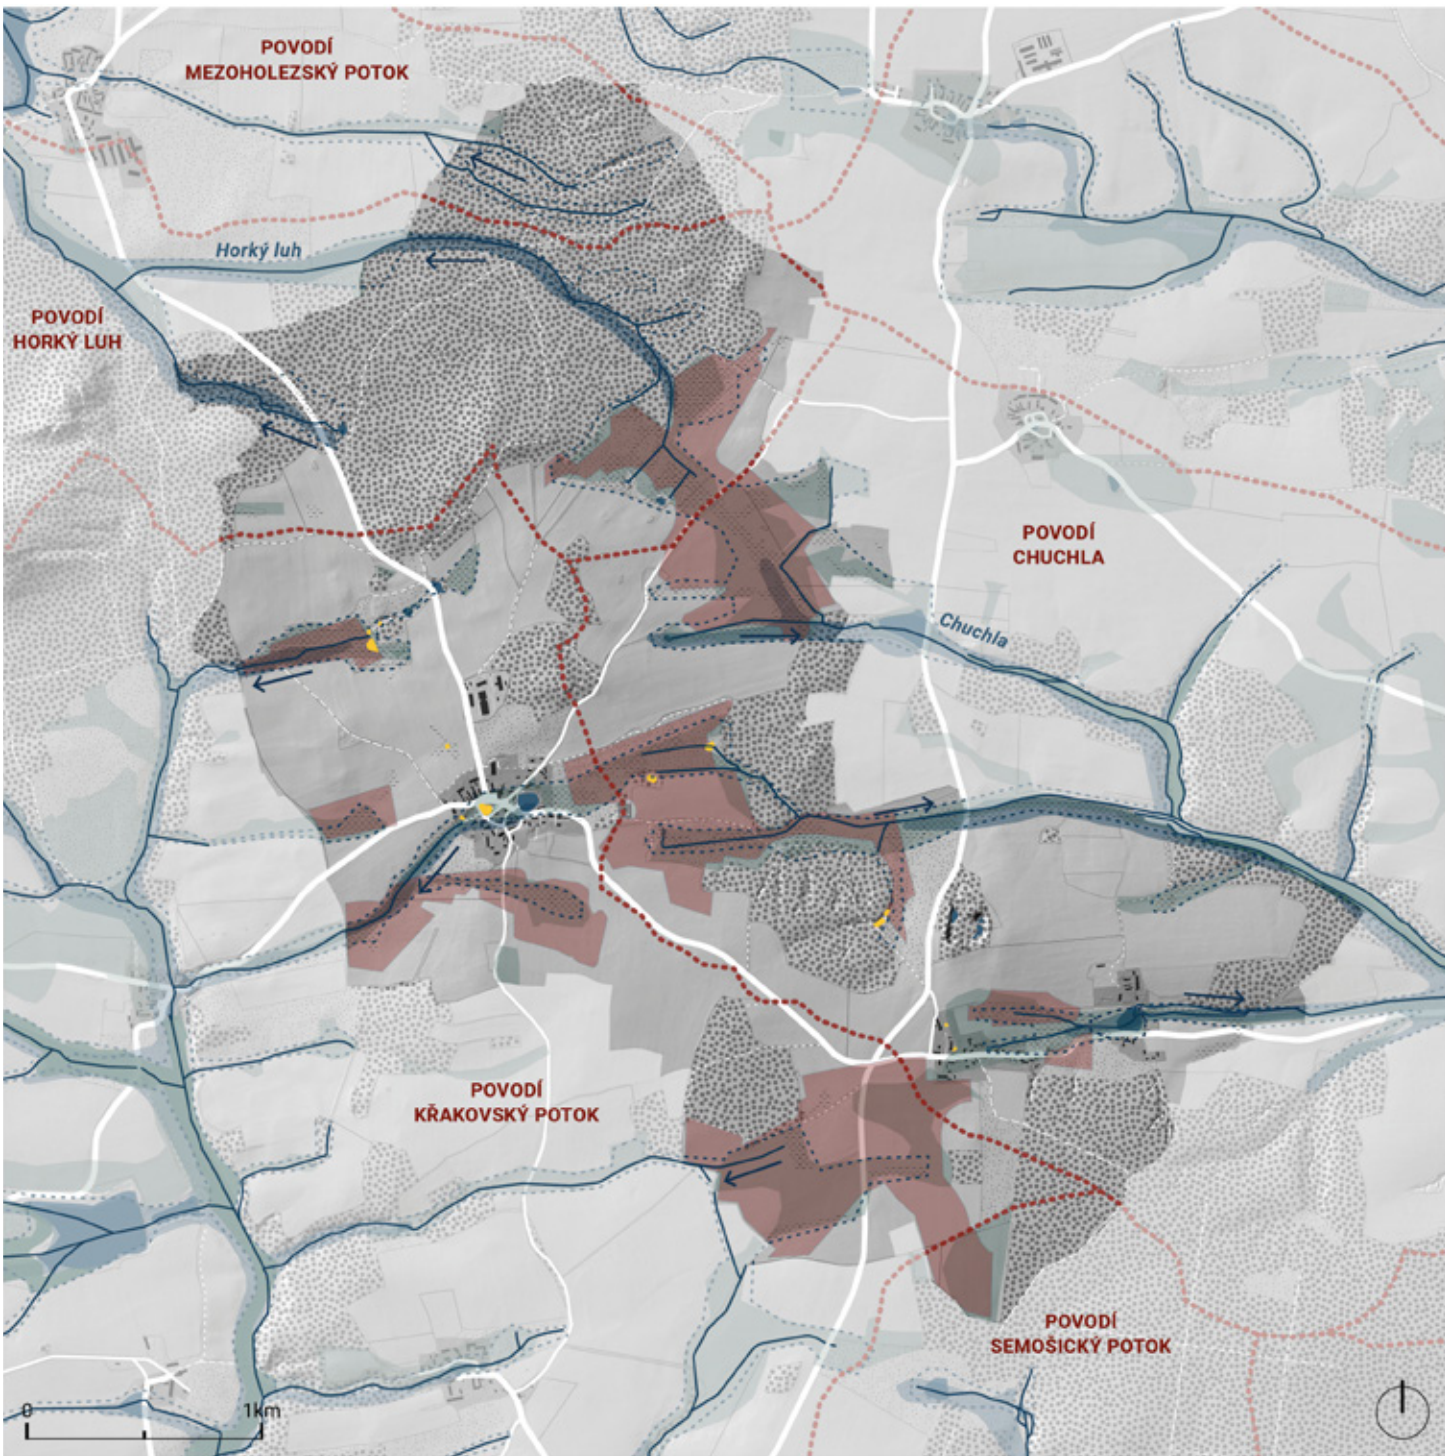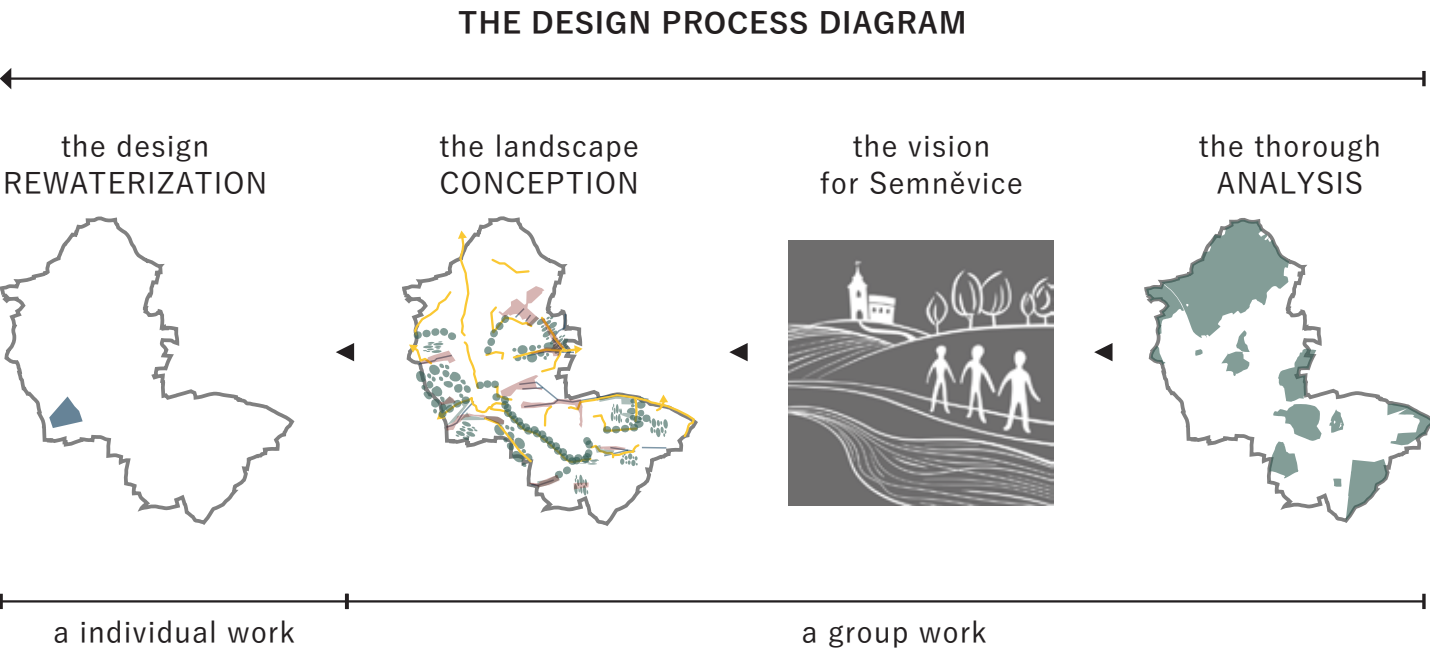


AN EXAMPLE OF ANALYTICAL DRAWING - The water regime analysis

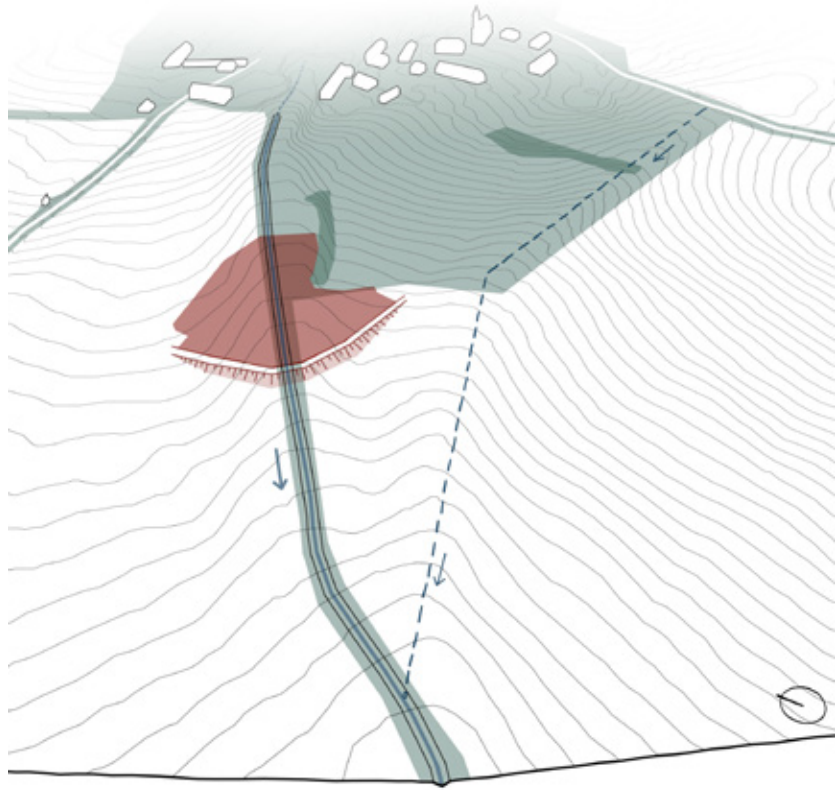

THE DIAGRAM OF THE PRESENT STATE








THE PHYSICAL MODEL

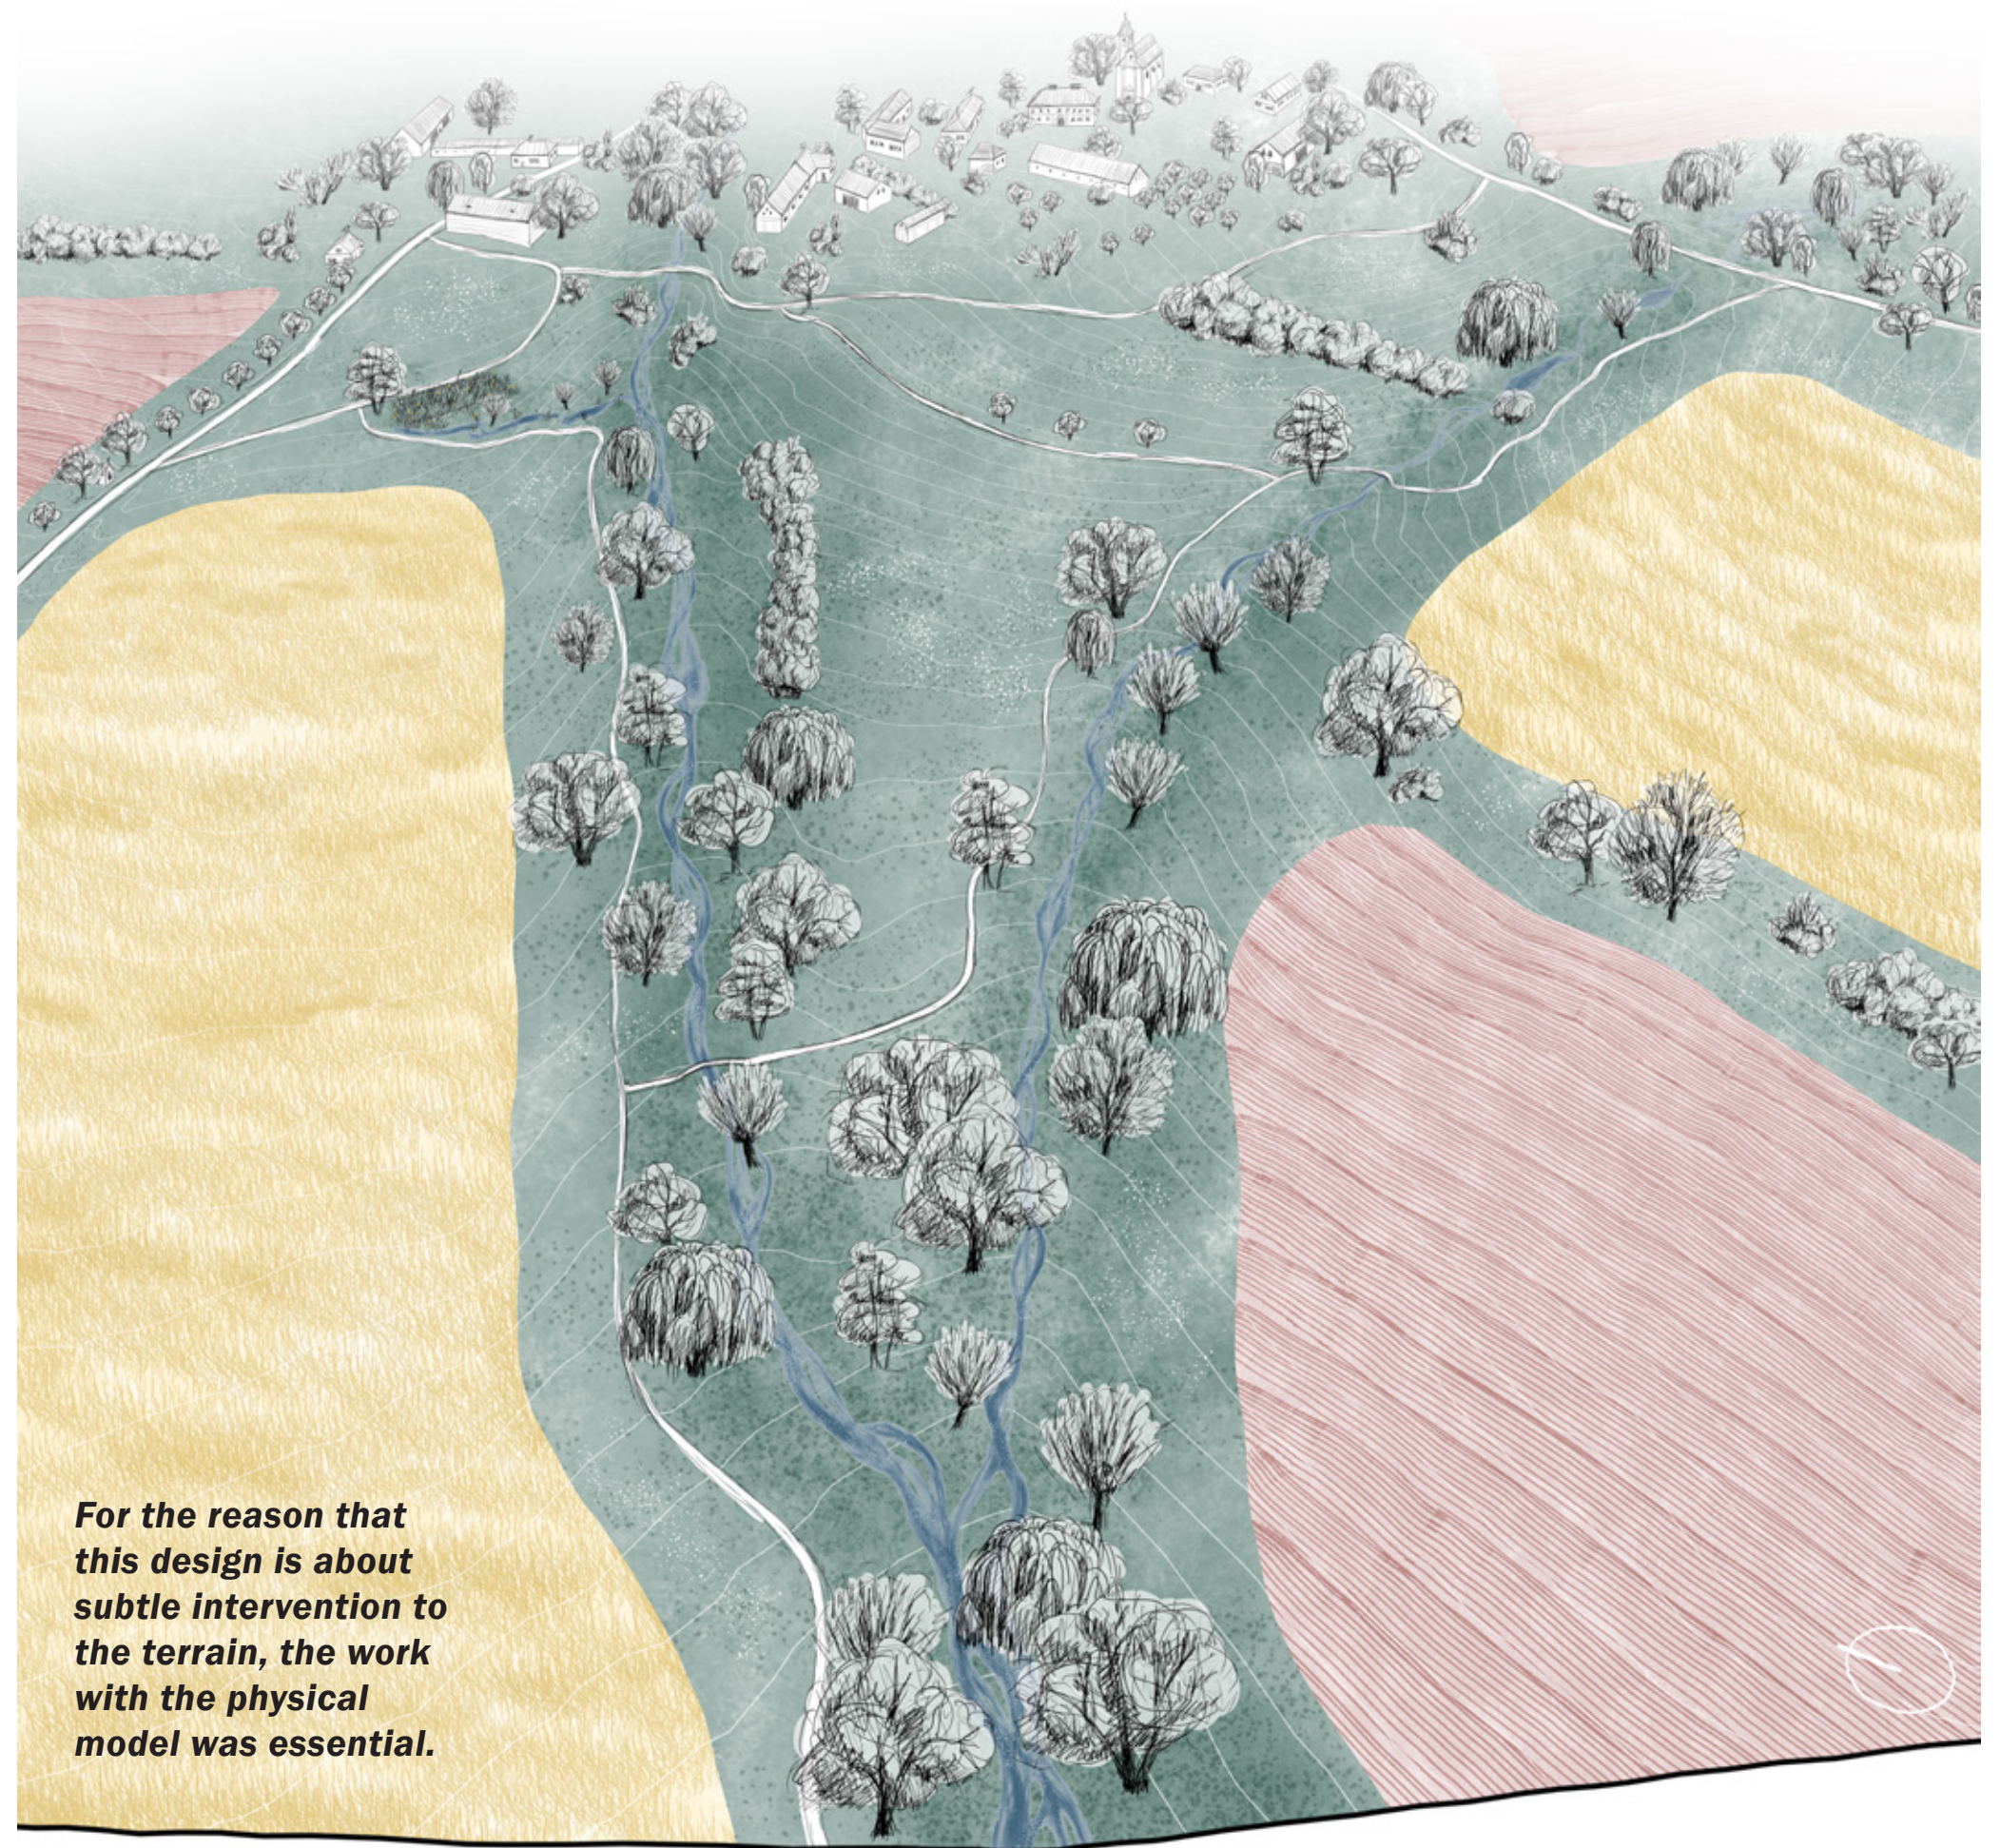

THE PERSPECTIVE DRAWING OF THE DESIGN

Since the task was based on real demands of the local municipality, within their aim to improve the environment, I tried to demonstrate the water-restoring principles properly.

The idea was that even if my design isn't built as a whole, individual citizens may pursue some actions to help the water regime on their own.

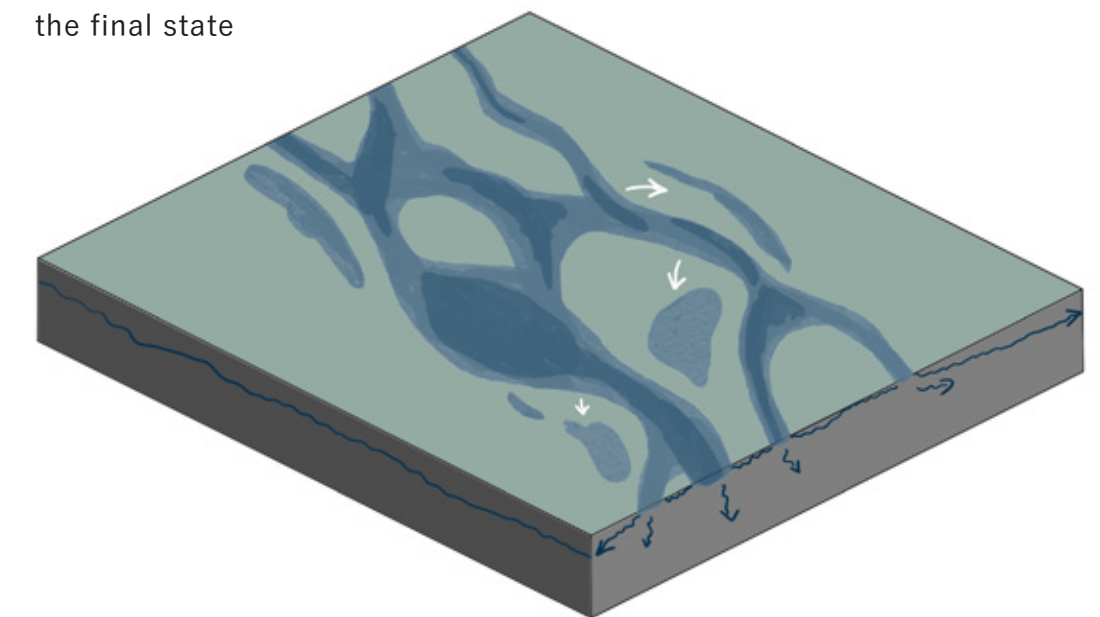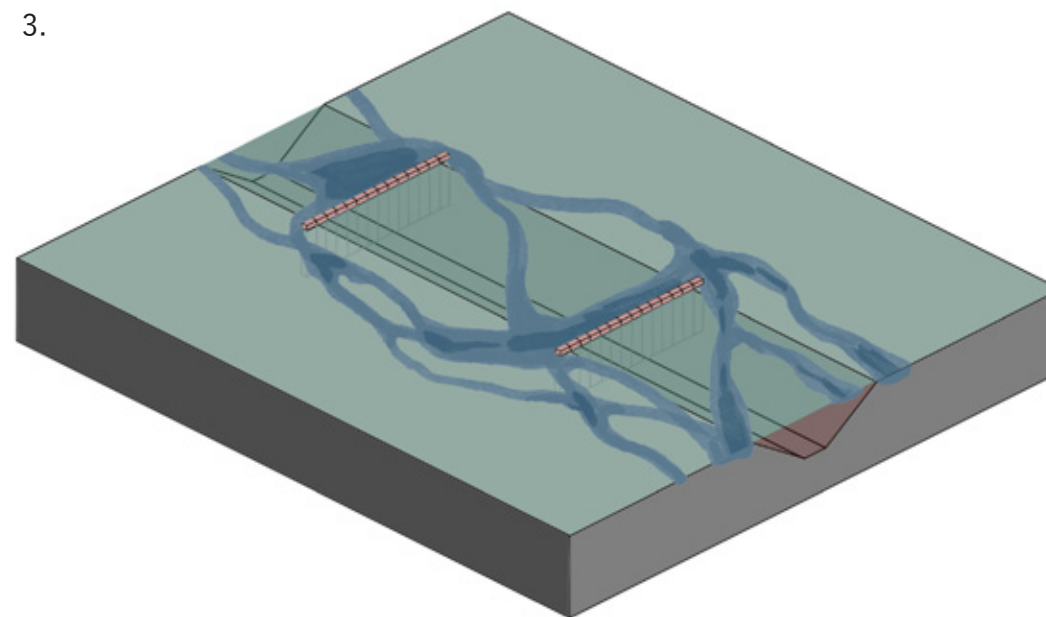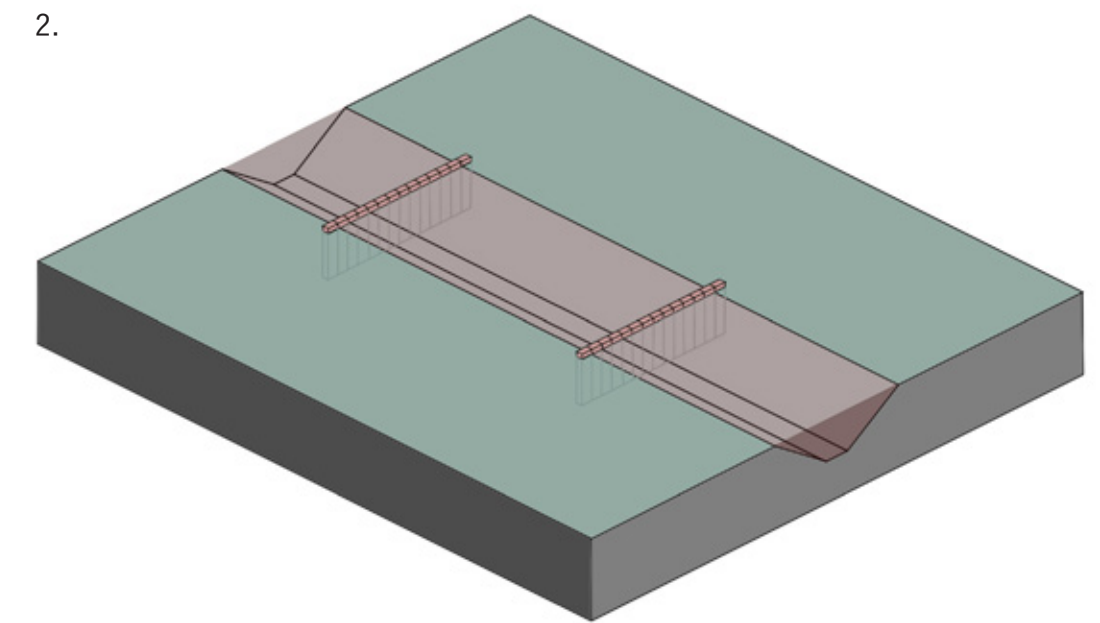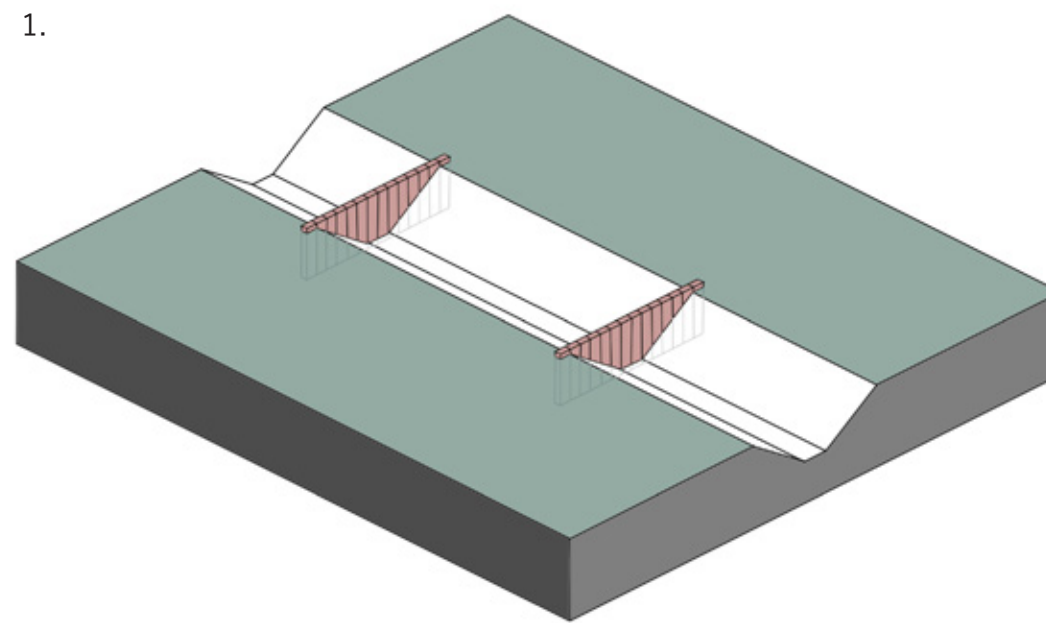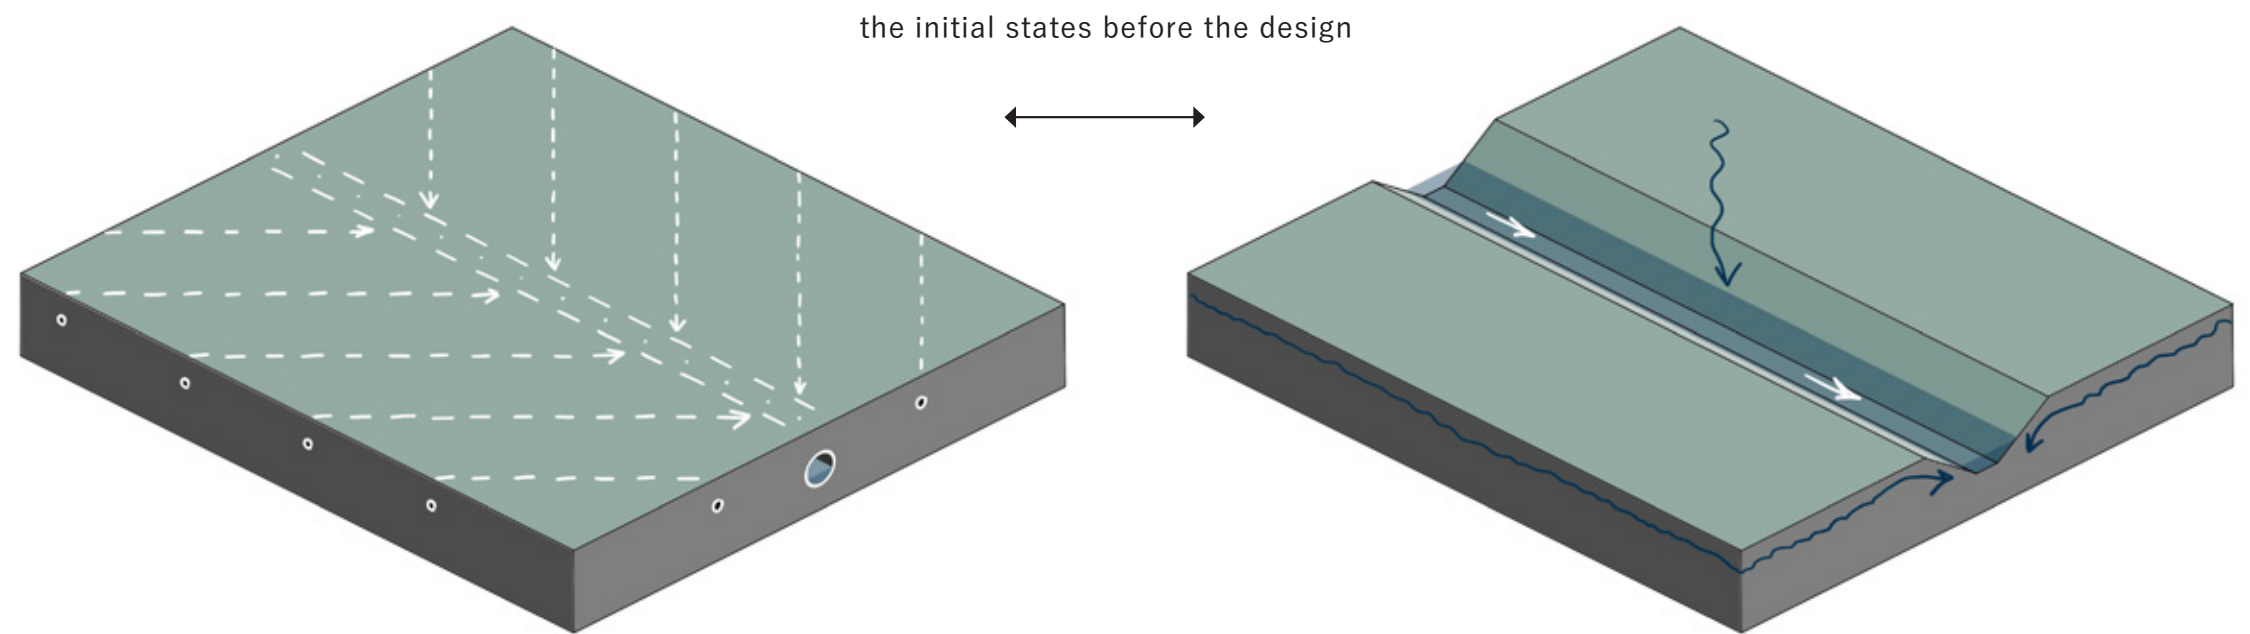

THE DIAGRAM OF THE SUGGESTED INTERVENTION

It shows how to get the water level closer to the ground level, to slow the flow, reinforce the groundwater reserve and support the ecosystem function.





***The project was presented to the citizens of the municipality.
In 2024 we won the Dean´s Award for the best landscape project of the faculty.***

ABSTRACT.

The aim of the design was to emerge from the landscape. This was accomplished through a process of abstraction—extracting the essential elements and using them as the foundation for the work, ensuring a relation to the place. The created urban tissue is shaped as an interpretation of the landscape, for it to make the place more readable for its visitors, fostering a deeper emotional connection.

Centralized to the top of the hill with a community center, the two axes continue as pedestrian streets, referring to the main street in the old city center. Important was the usage of the partly opened block, with apartment buildings on the edges and row-houses in the middle. Therefore, the sun exposure and sheltering from the wind is achieved, as well as the cosy courtyards creating communities.


VISUALIZATION

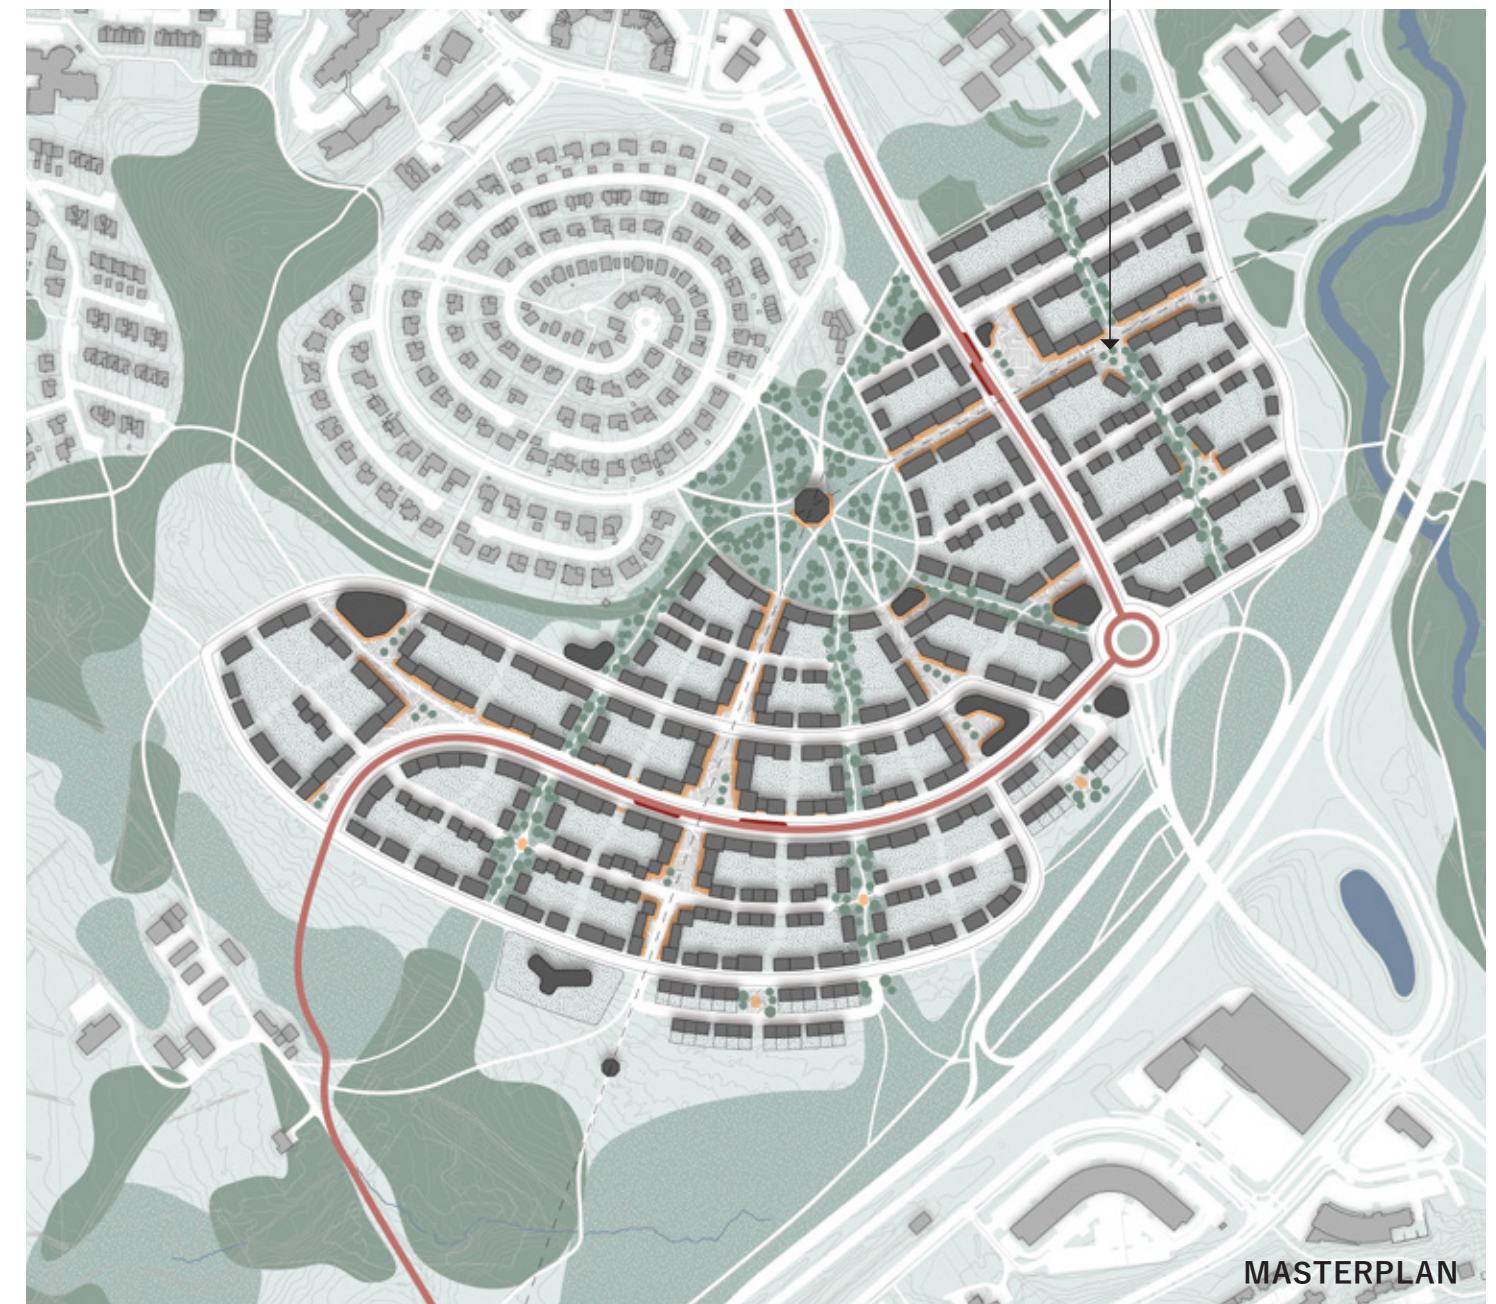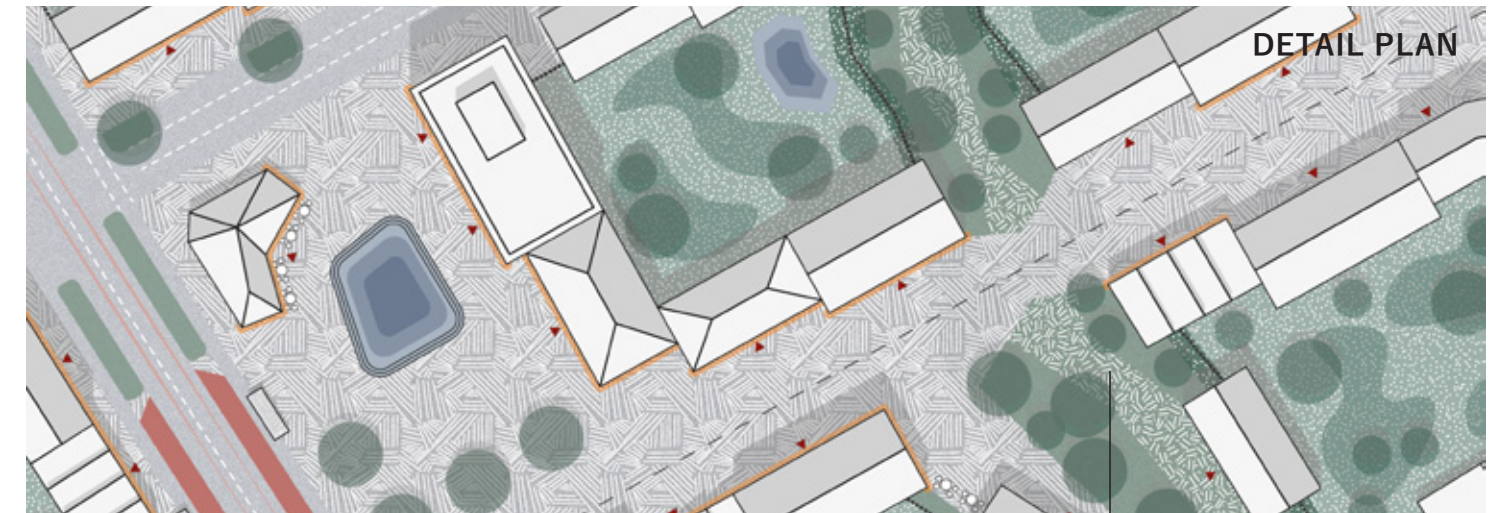

INFRASTRUCTURE DIAGRAM



AXONOMETRY OF THE BLOCK PRINCIPLE

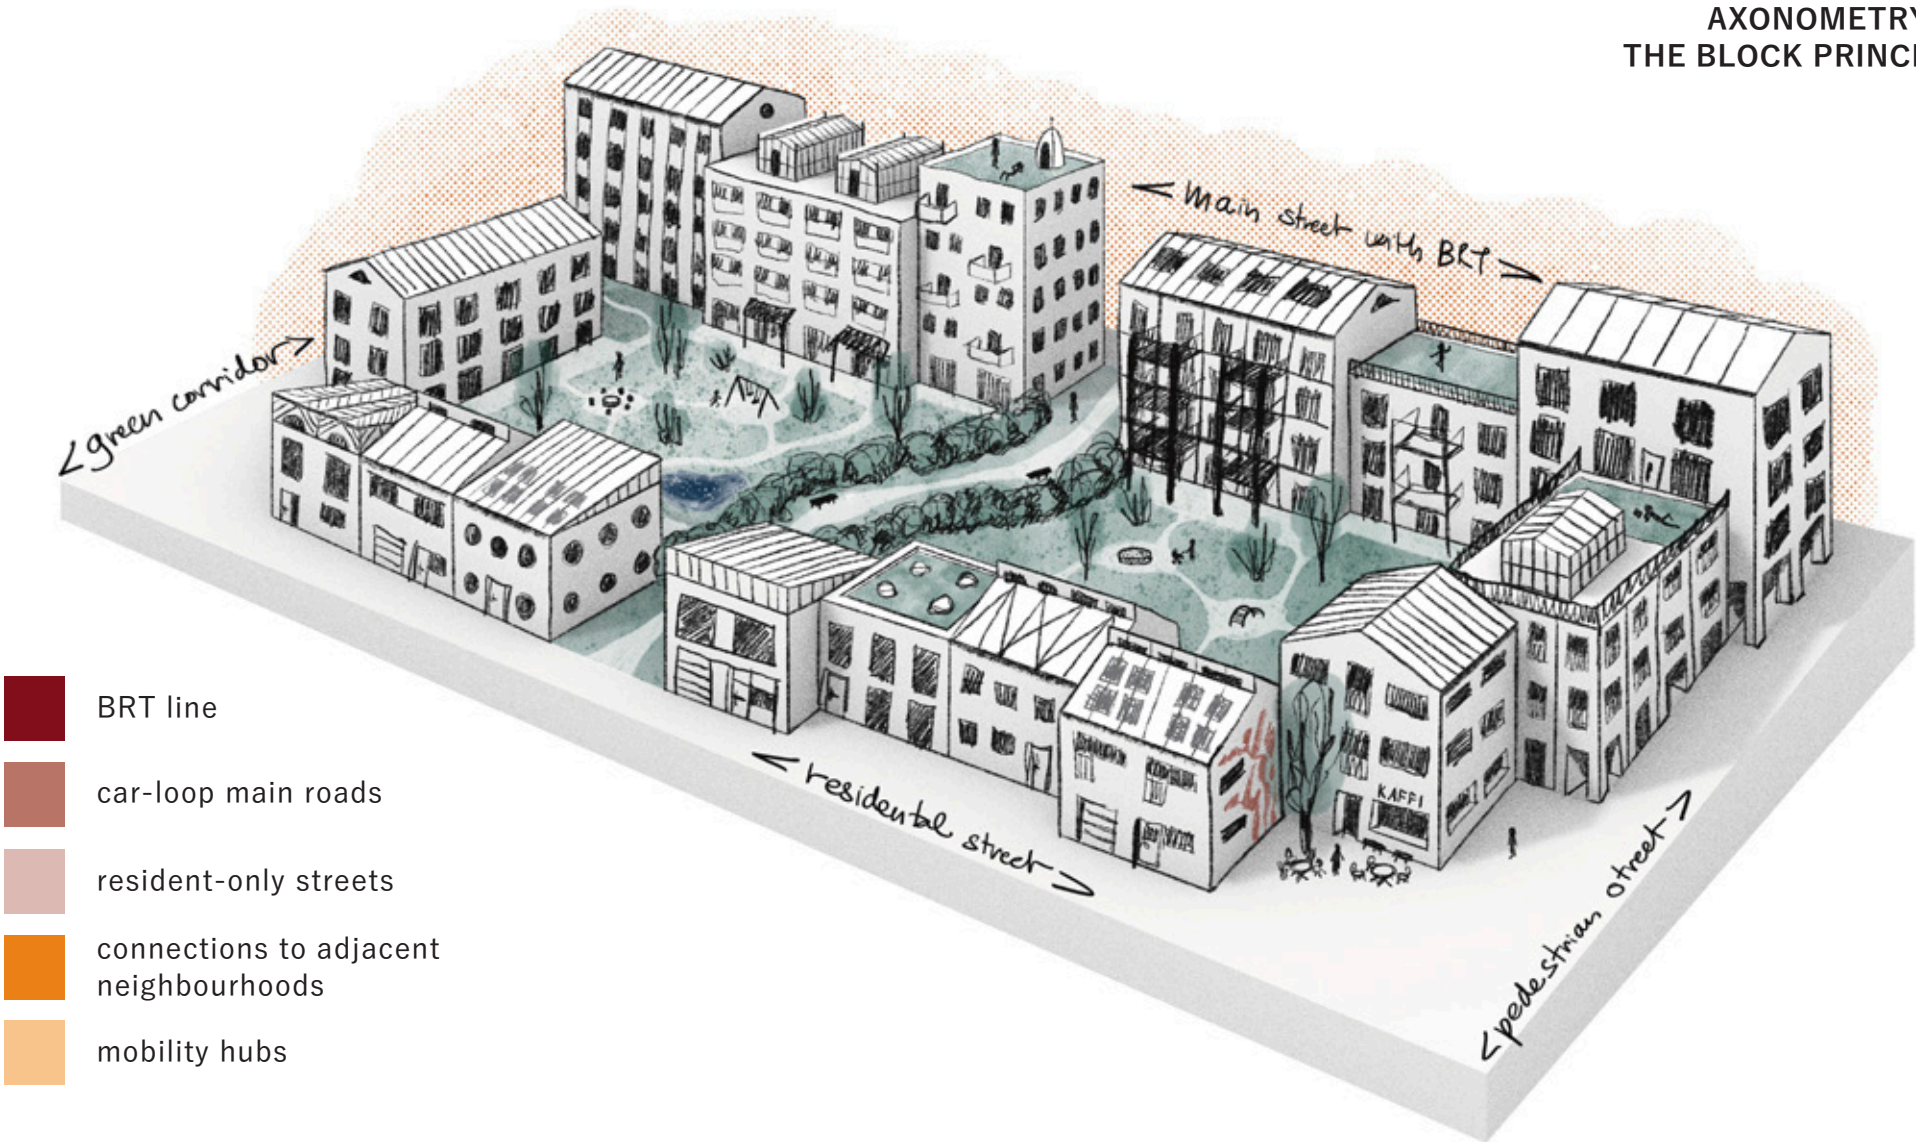

VISUALIZATIONS





WATERSCAPE


Milan was once the city of water canals, such as Venice. The task of the international competition was to find how to reopen them and how the public space around them should look like. Particularly a street with a park square, connecting the future archeological park with a water basin and former port – Darsena.

With the use of many smaller islands, the design offers a more intimate contact with the water level in numerous forms. The spatial concept is also formed by two paths in the main transit directions, to be pedestrian friendly. Thanks to modest playing features, uncommon opportunities for exercise and a café half-hidden in the terrain, it's a public space for everyone.


This project demonstrates a work with mid-scale urban landscape.
It was a challenging task because, despite my limited experience, I tried an official architectural competition.

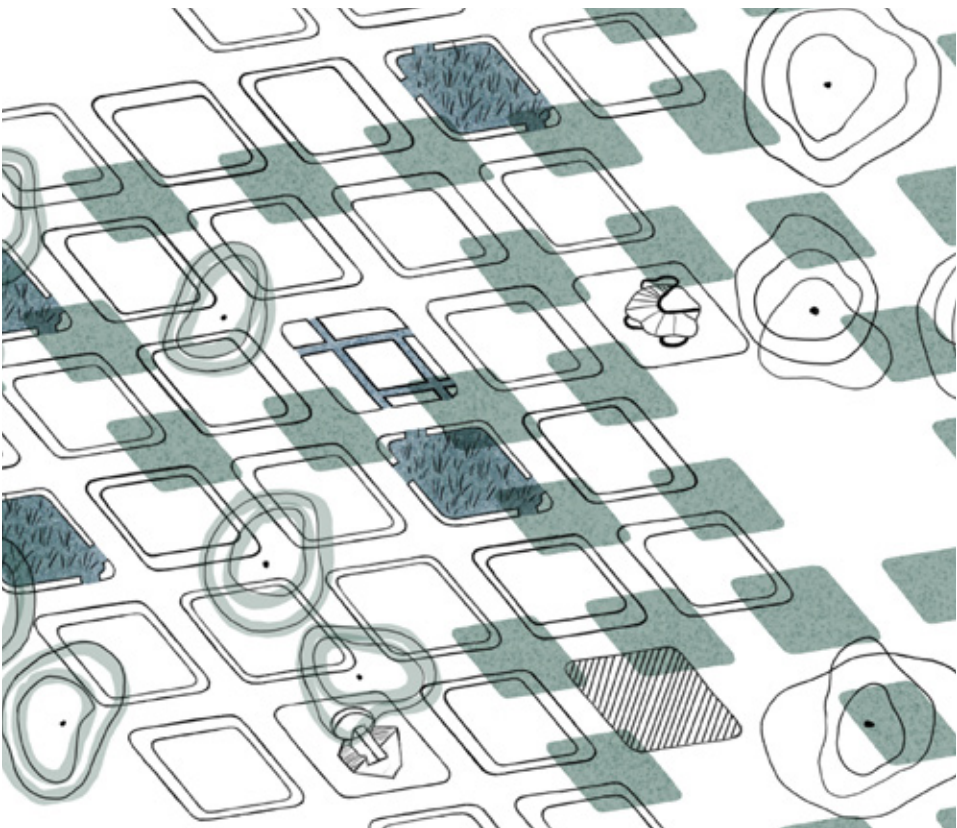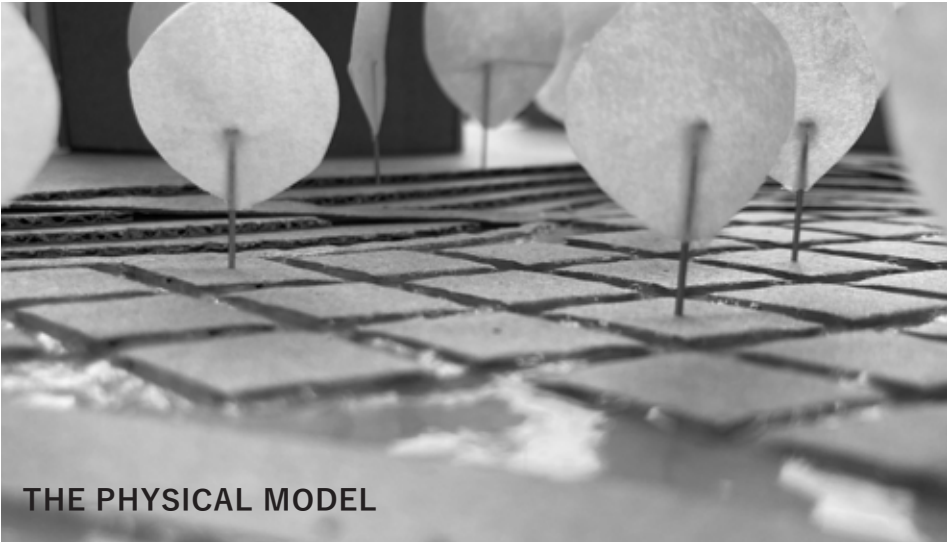


WATER FLOW

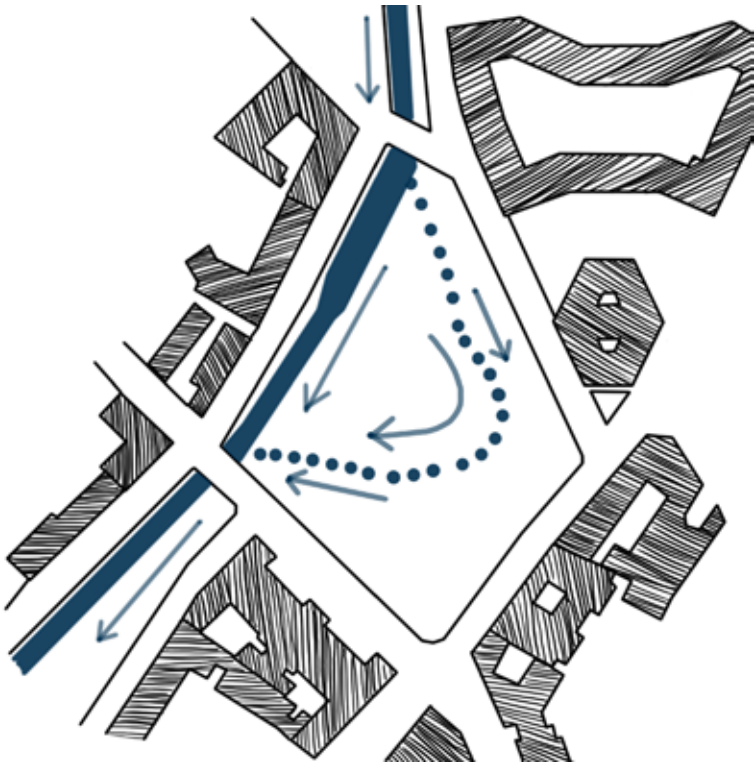

SHALLOW AMPHITHEATRE TERRAIN

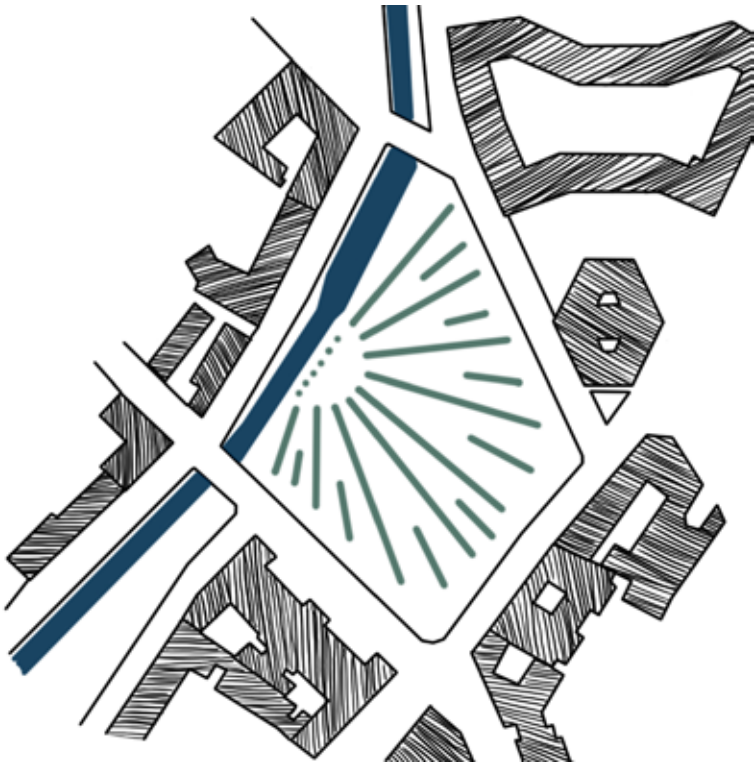



MAIN PEDESTRIAN DIRECTION

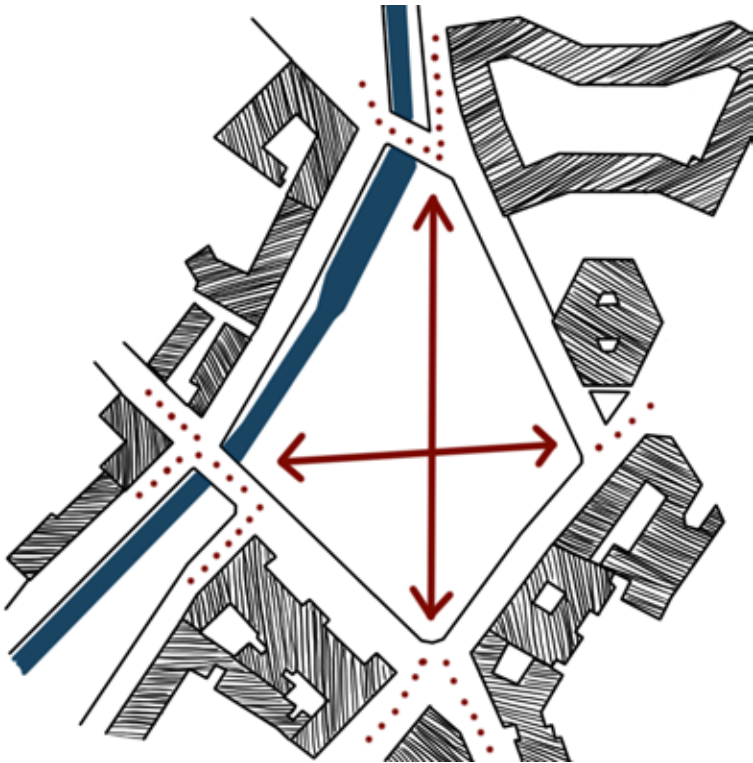


THE DIAGRAM OF THE WATERSCAPE CONCEPT

A MASTERPLAN
CUTOUT

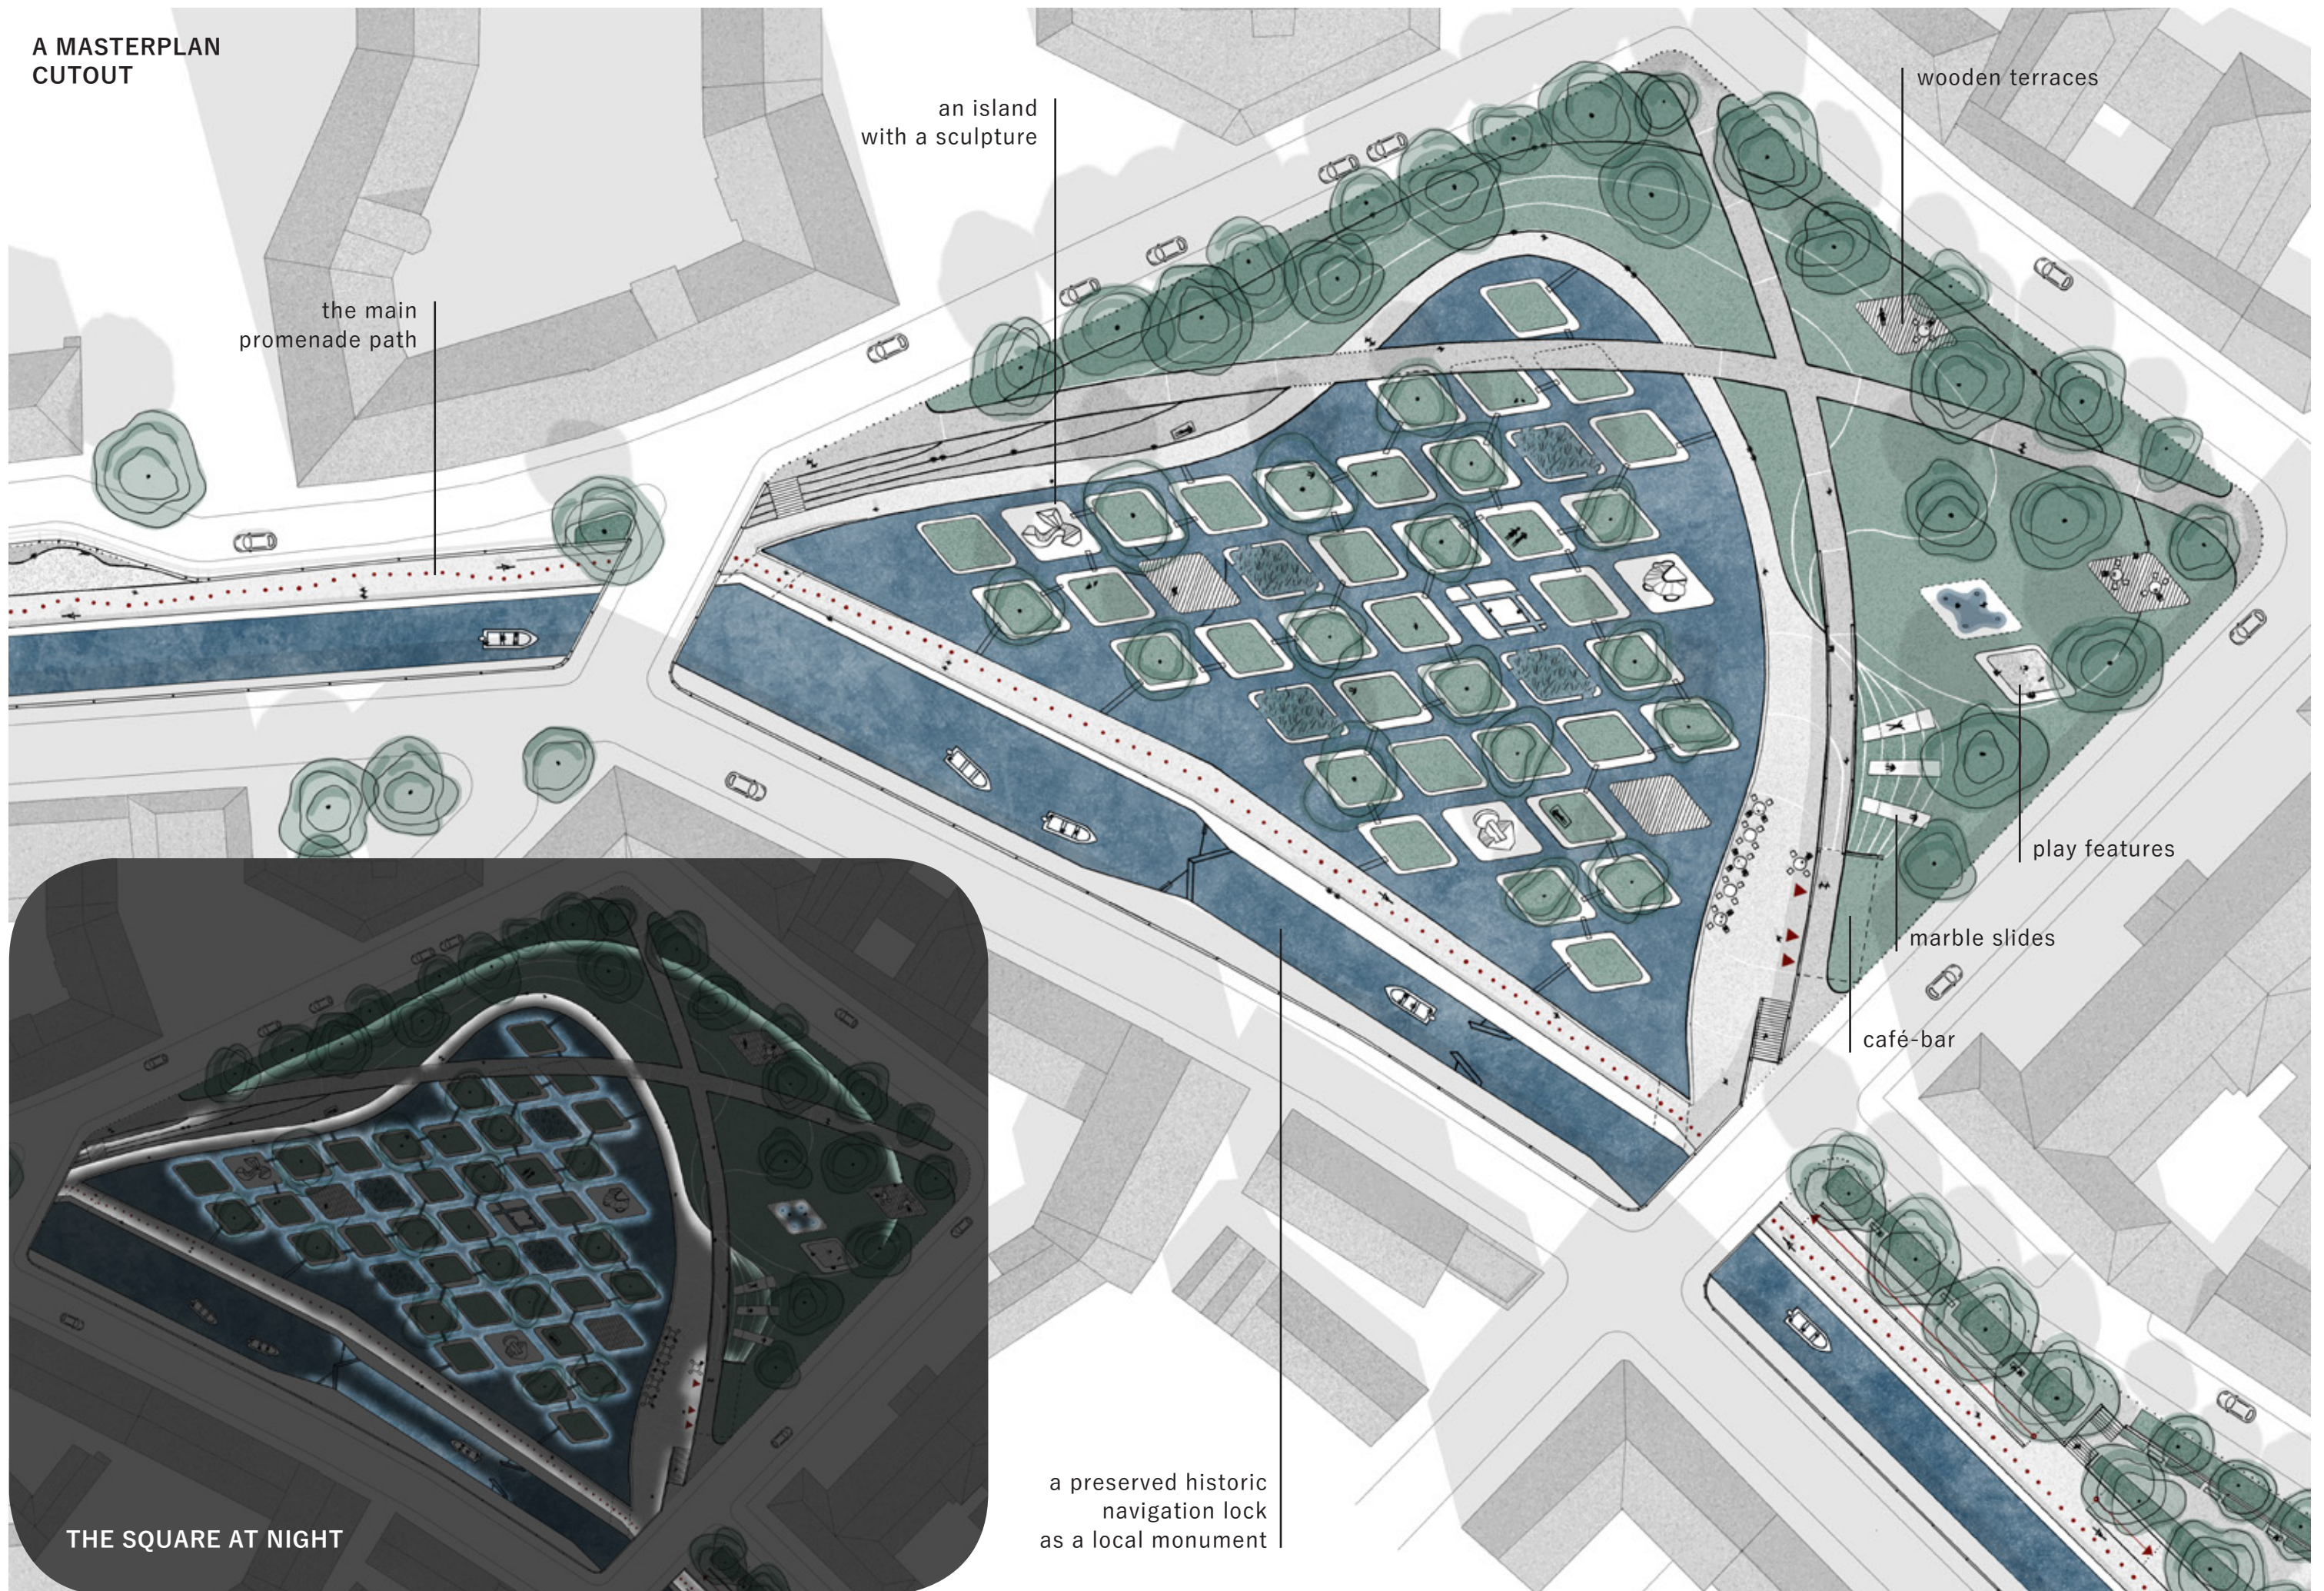

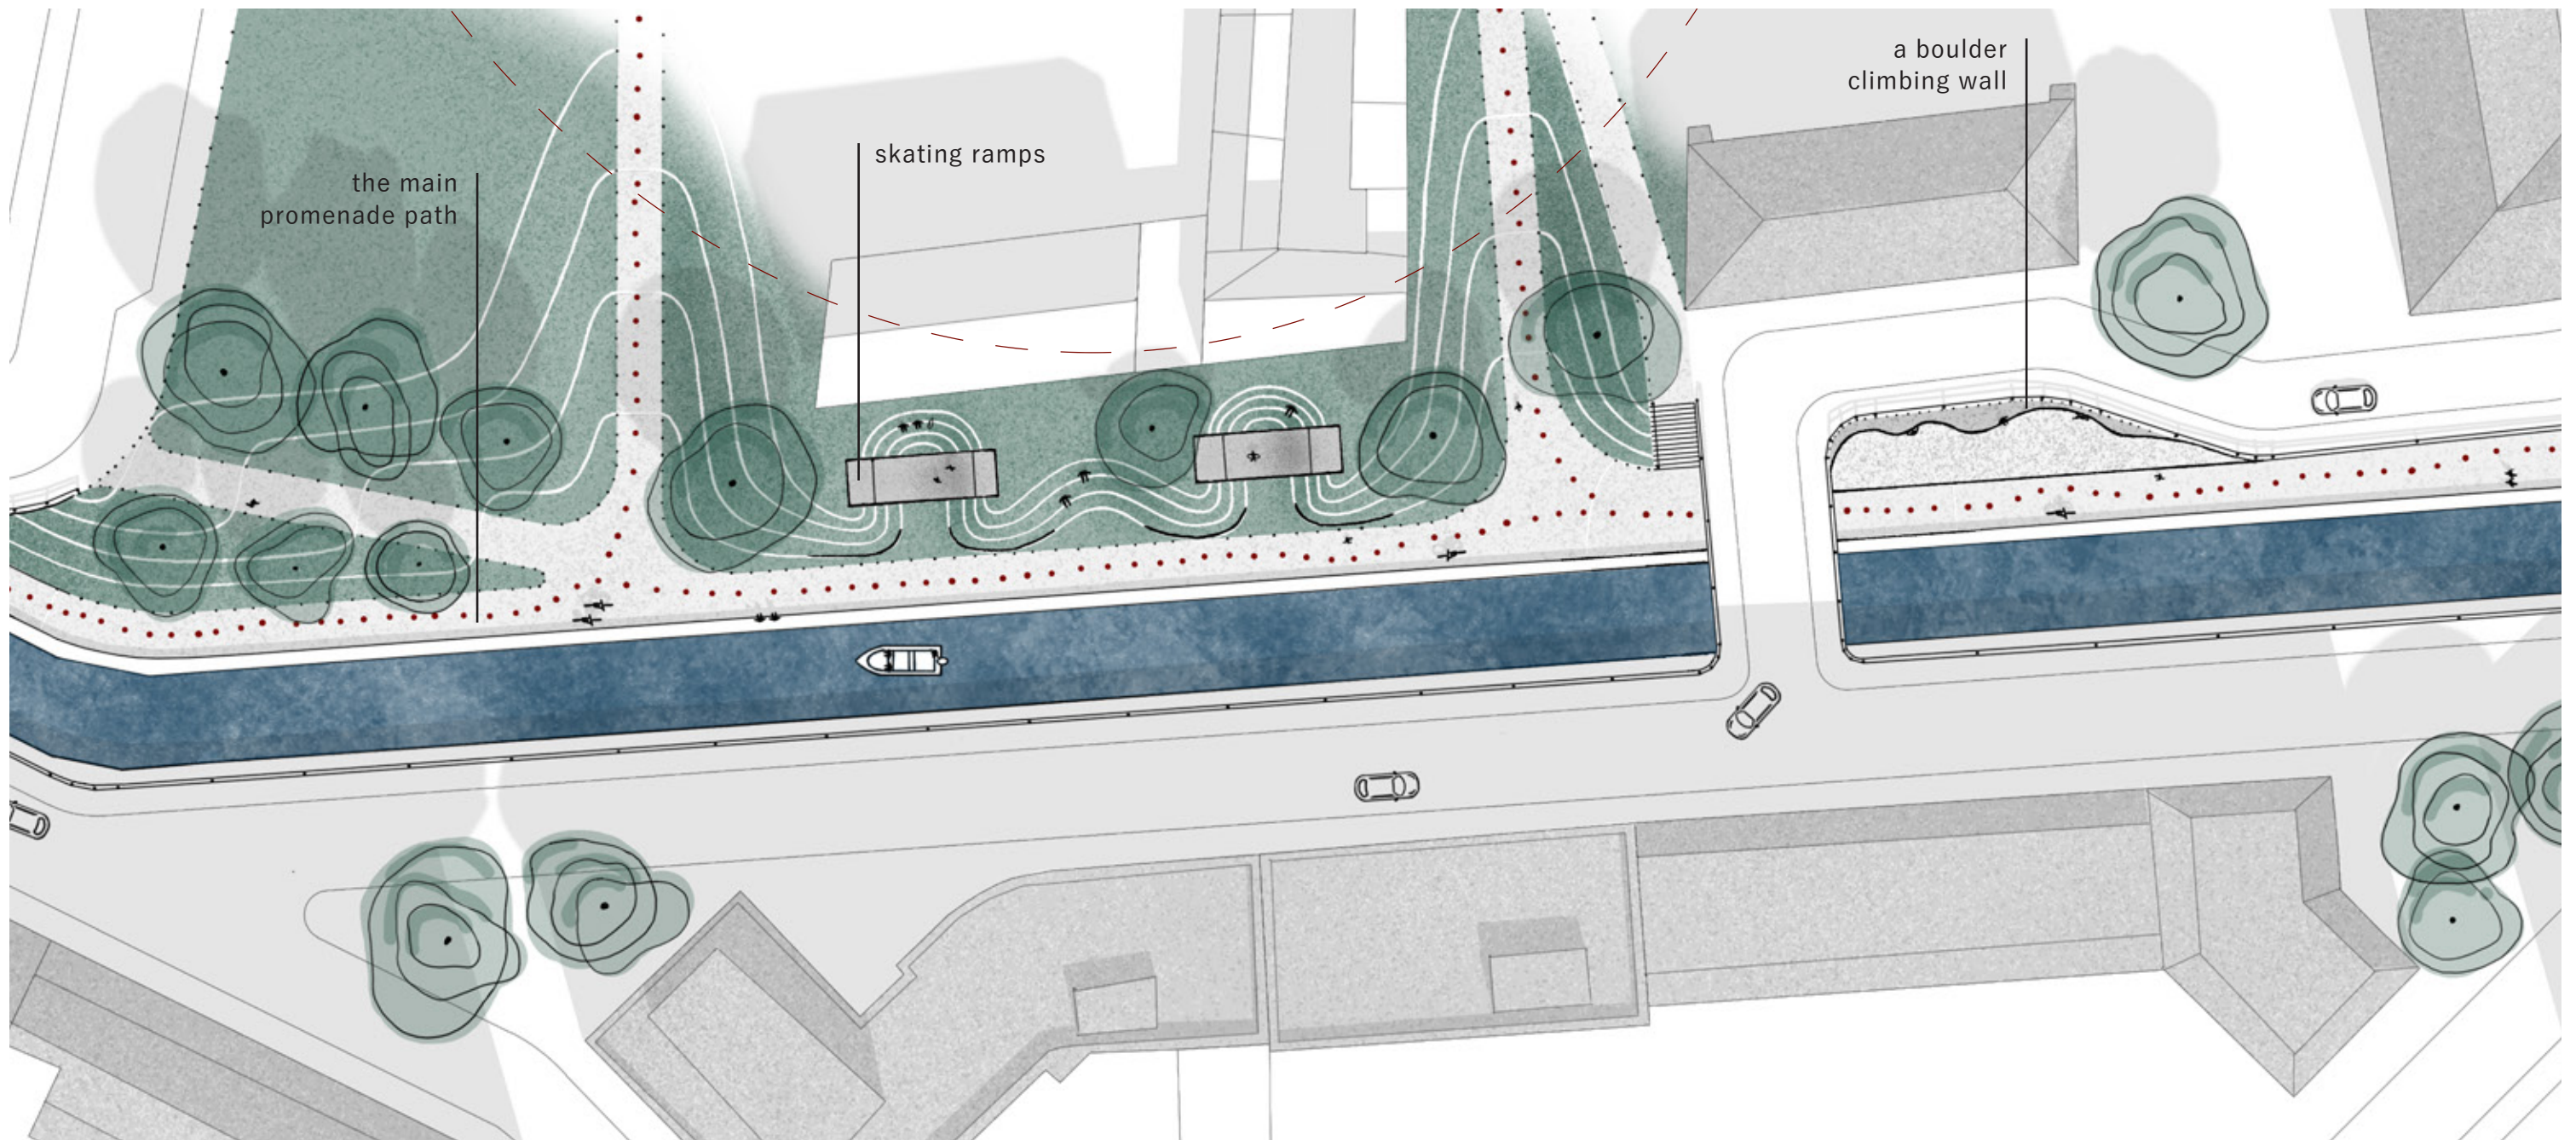

A MASTERPLAN AND SECTION CUTOUTS

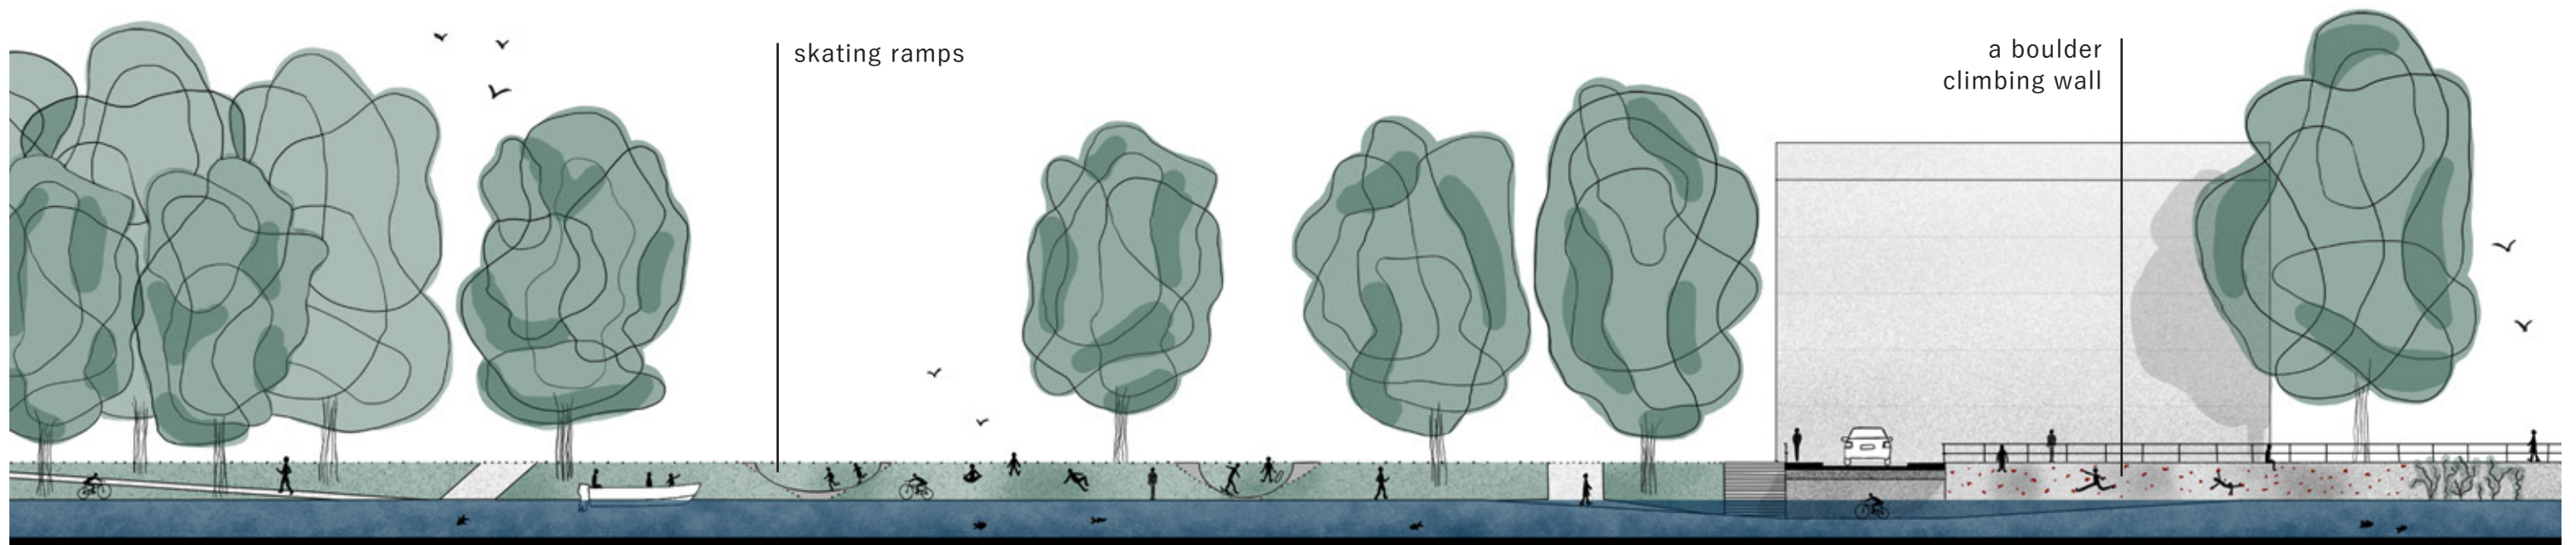


STEEP GARDEN

This project is a redevelopment design for a garden around a family house in Prague's Střešovice district, subsequently processed into project documentation. The project's plot is very steep, so the design works with the terrain to create more usable spaces. The concept is based on simplicity, based on the small spaces of the garden.

With this task, a challenge arose due to the lack of documentation. I had to conduct a land survey and 3D scanning to obtain the necessary measurements and data to draw a masterplan.

PRE-DESIGN SKETCHES

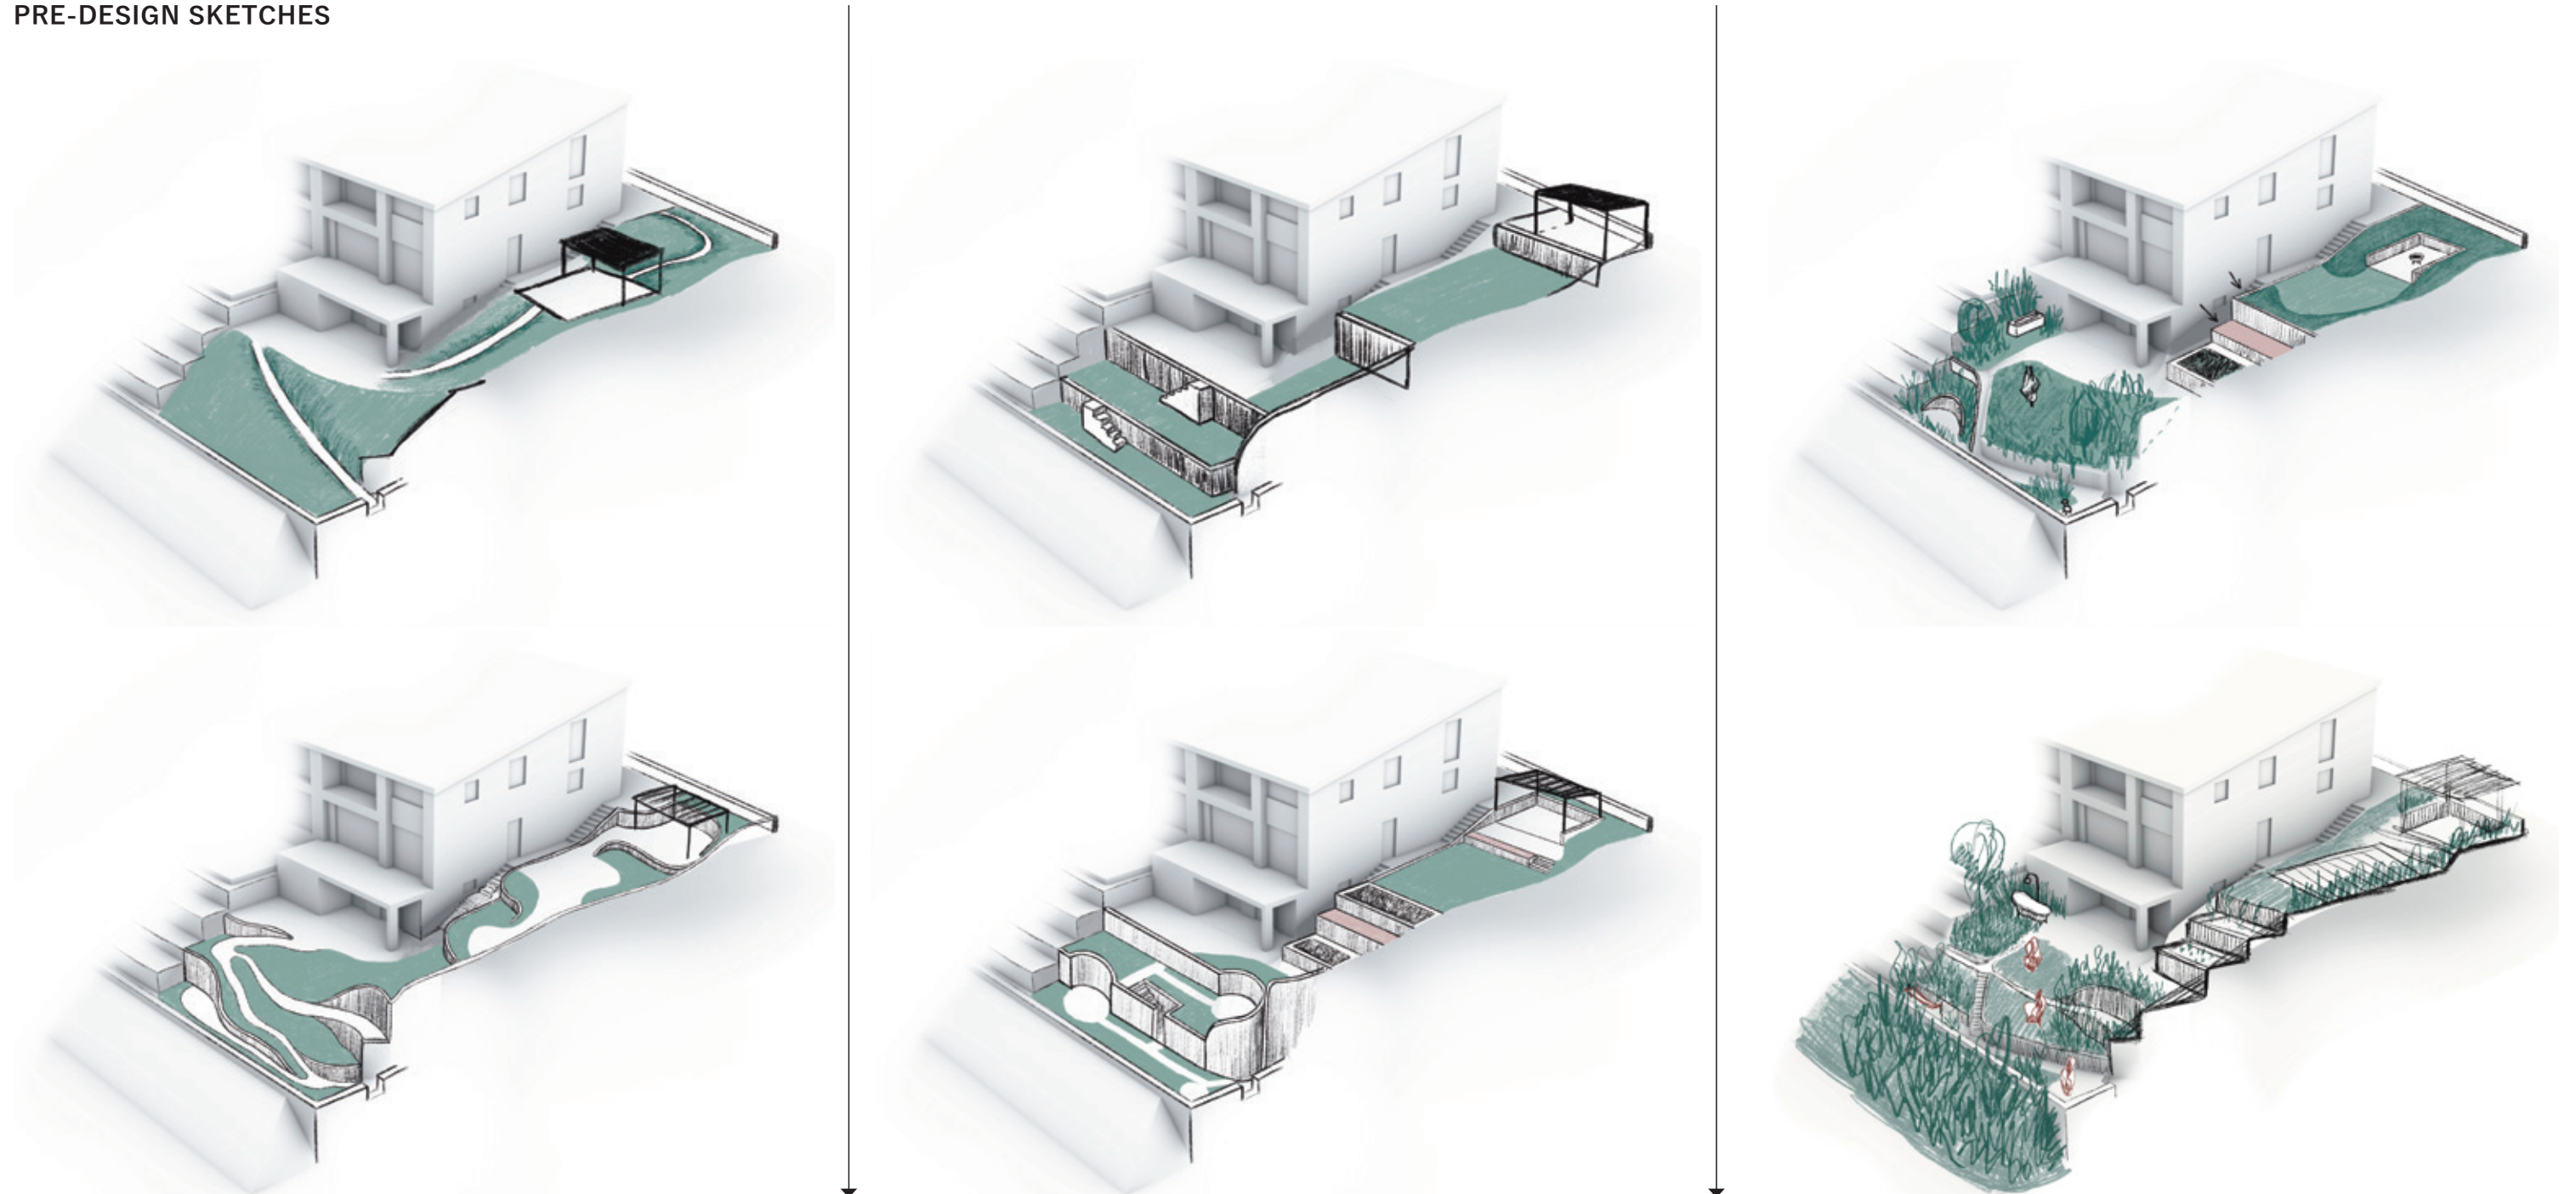


FINAL DESIGN




a bathtub for cooling
after sauna

a meditation room

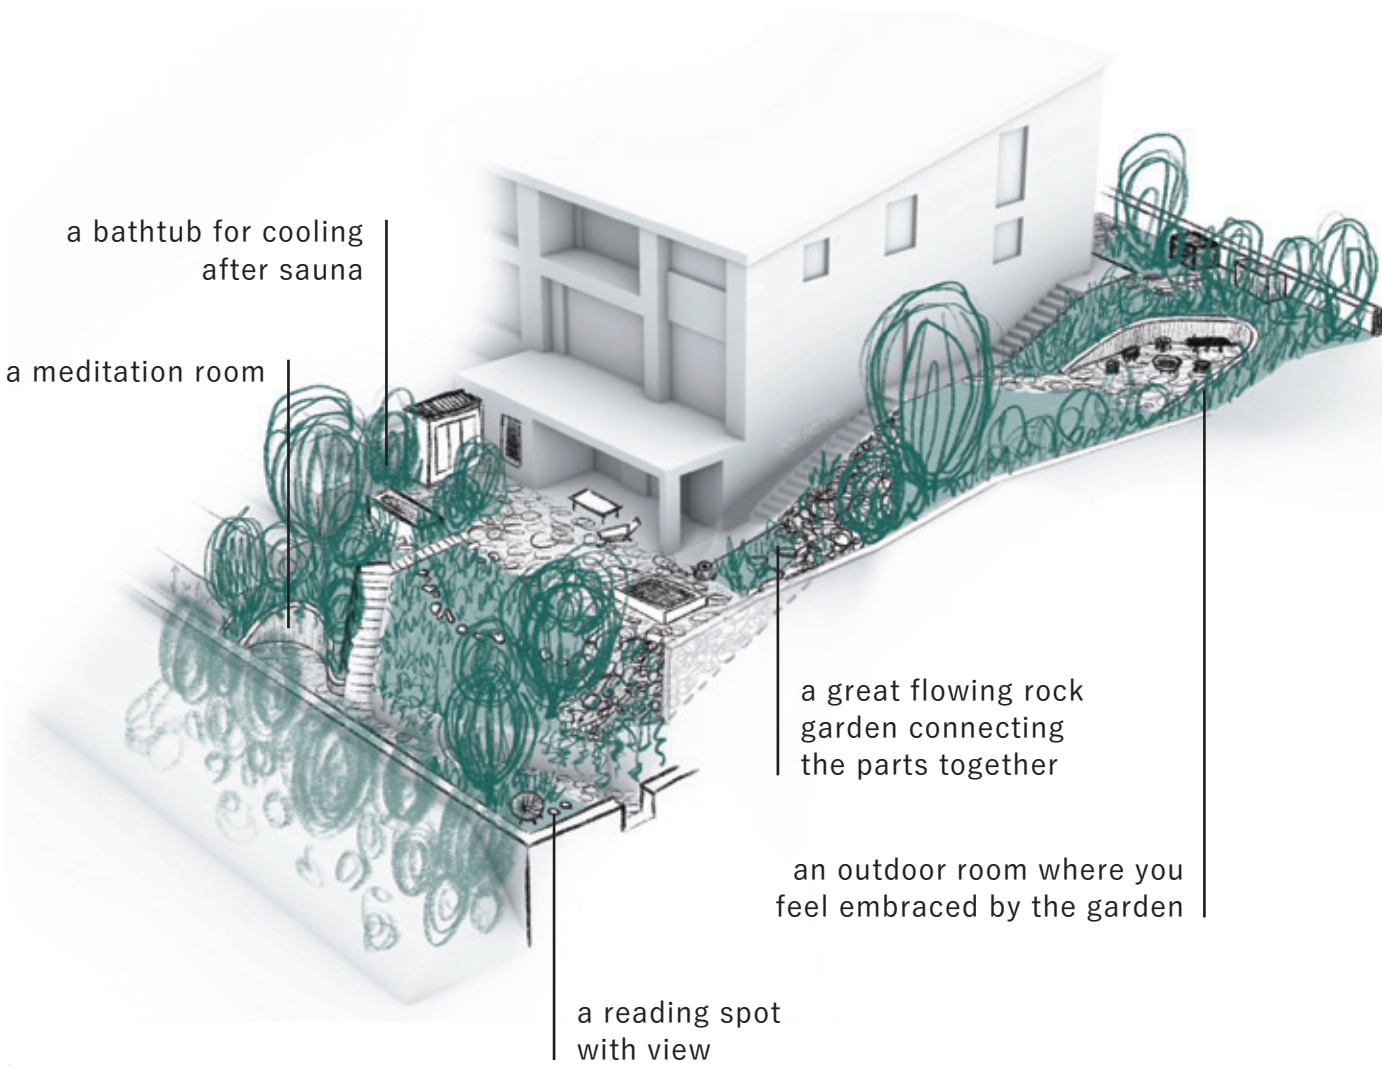


a great flowing rock
garden connecting
the parts together

an outdoor room where you
feel embraced by the garden

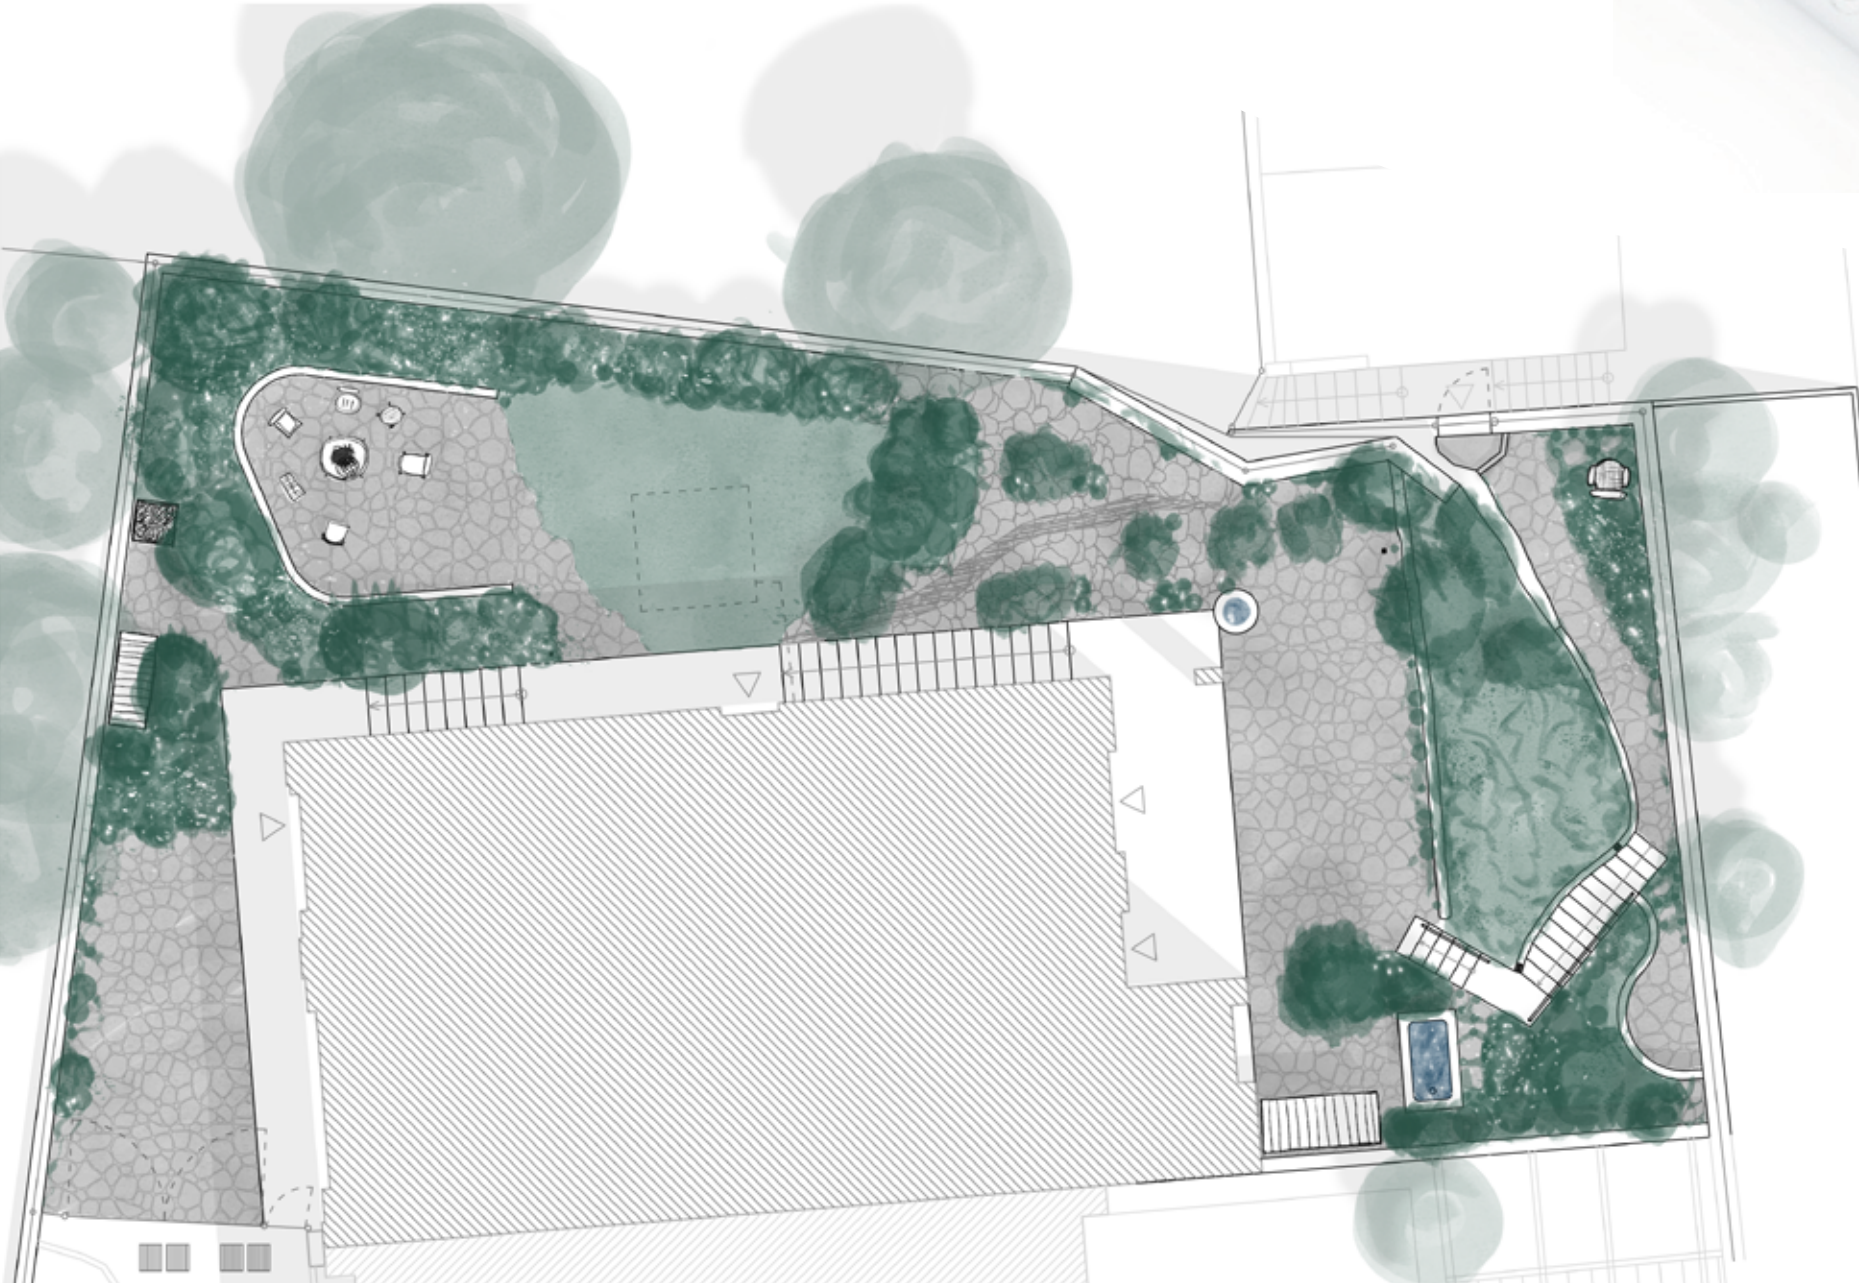


The final aesthetic of the design is inspired by early 20th-century urban villa gardens, for example by the use of evergreen trees. The project creates cozy rooms that invite you to spend the time in the garden, rather than just looking at it. Despite its small size, the garden offers spaces for socializing or quiet solitude for all house residents.

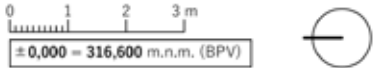

M 1:50 legenda



SKLADBA TRÁVNÍKU
M 1:10

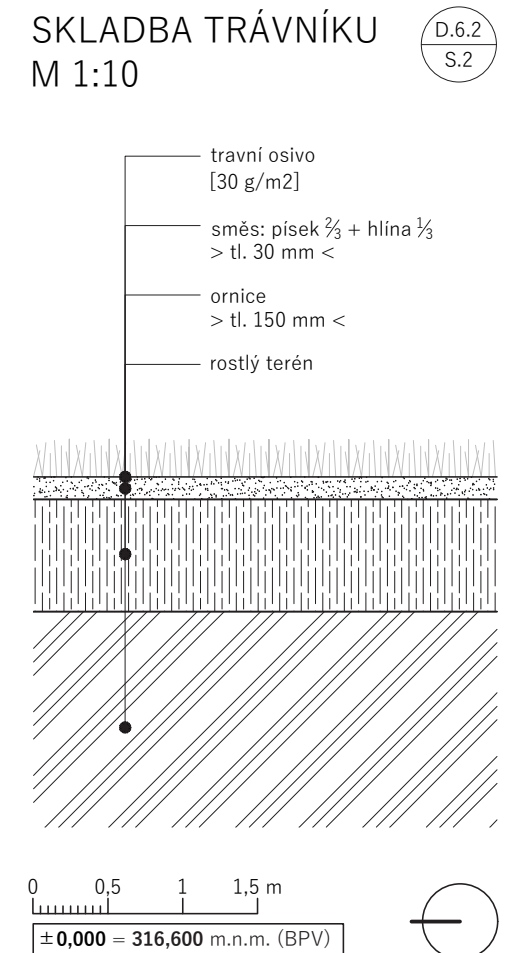

THE NEW LANDSCAPE OF HSR

The subject of the thesis is the design of a territorial transformation concept in connection with the future construction of the high-speed railway RS4 – Podřipsko II section. The work examines how to ideally integrate a linear infrastructure project into the agricultural landscape adjacent to the Elbe, using a holistic landscape-architecture approach. It also includes exploring tools that allow the intervention, even at a large scale, to go beyond purely functional solutions — towards a coherent concept and an aesthetic intention.

THEMATIC COLLAGE

